


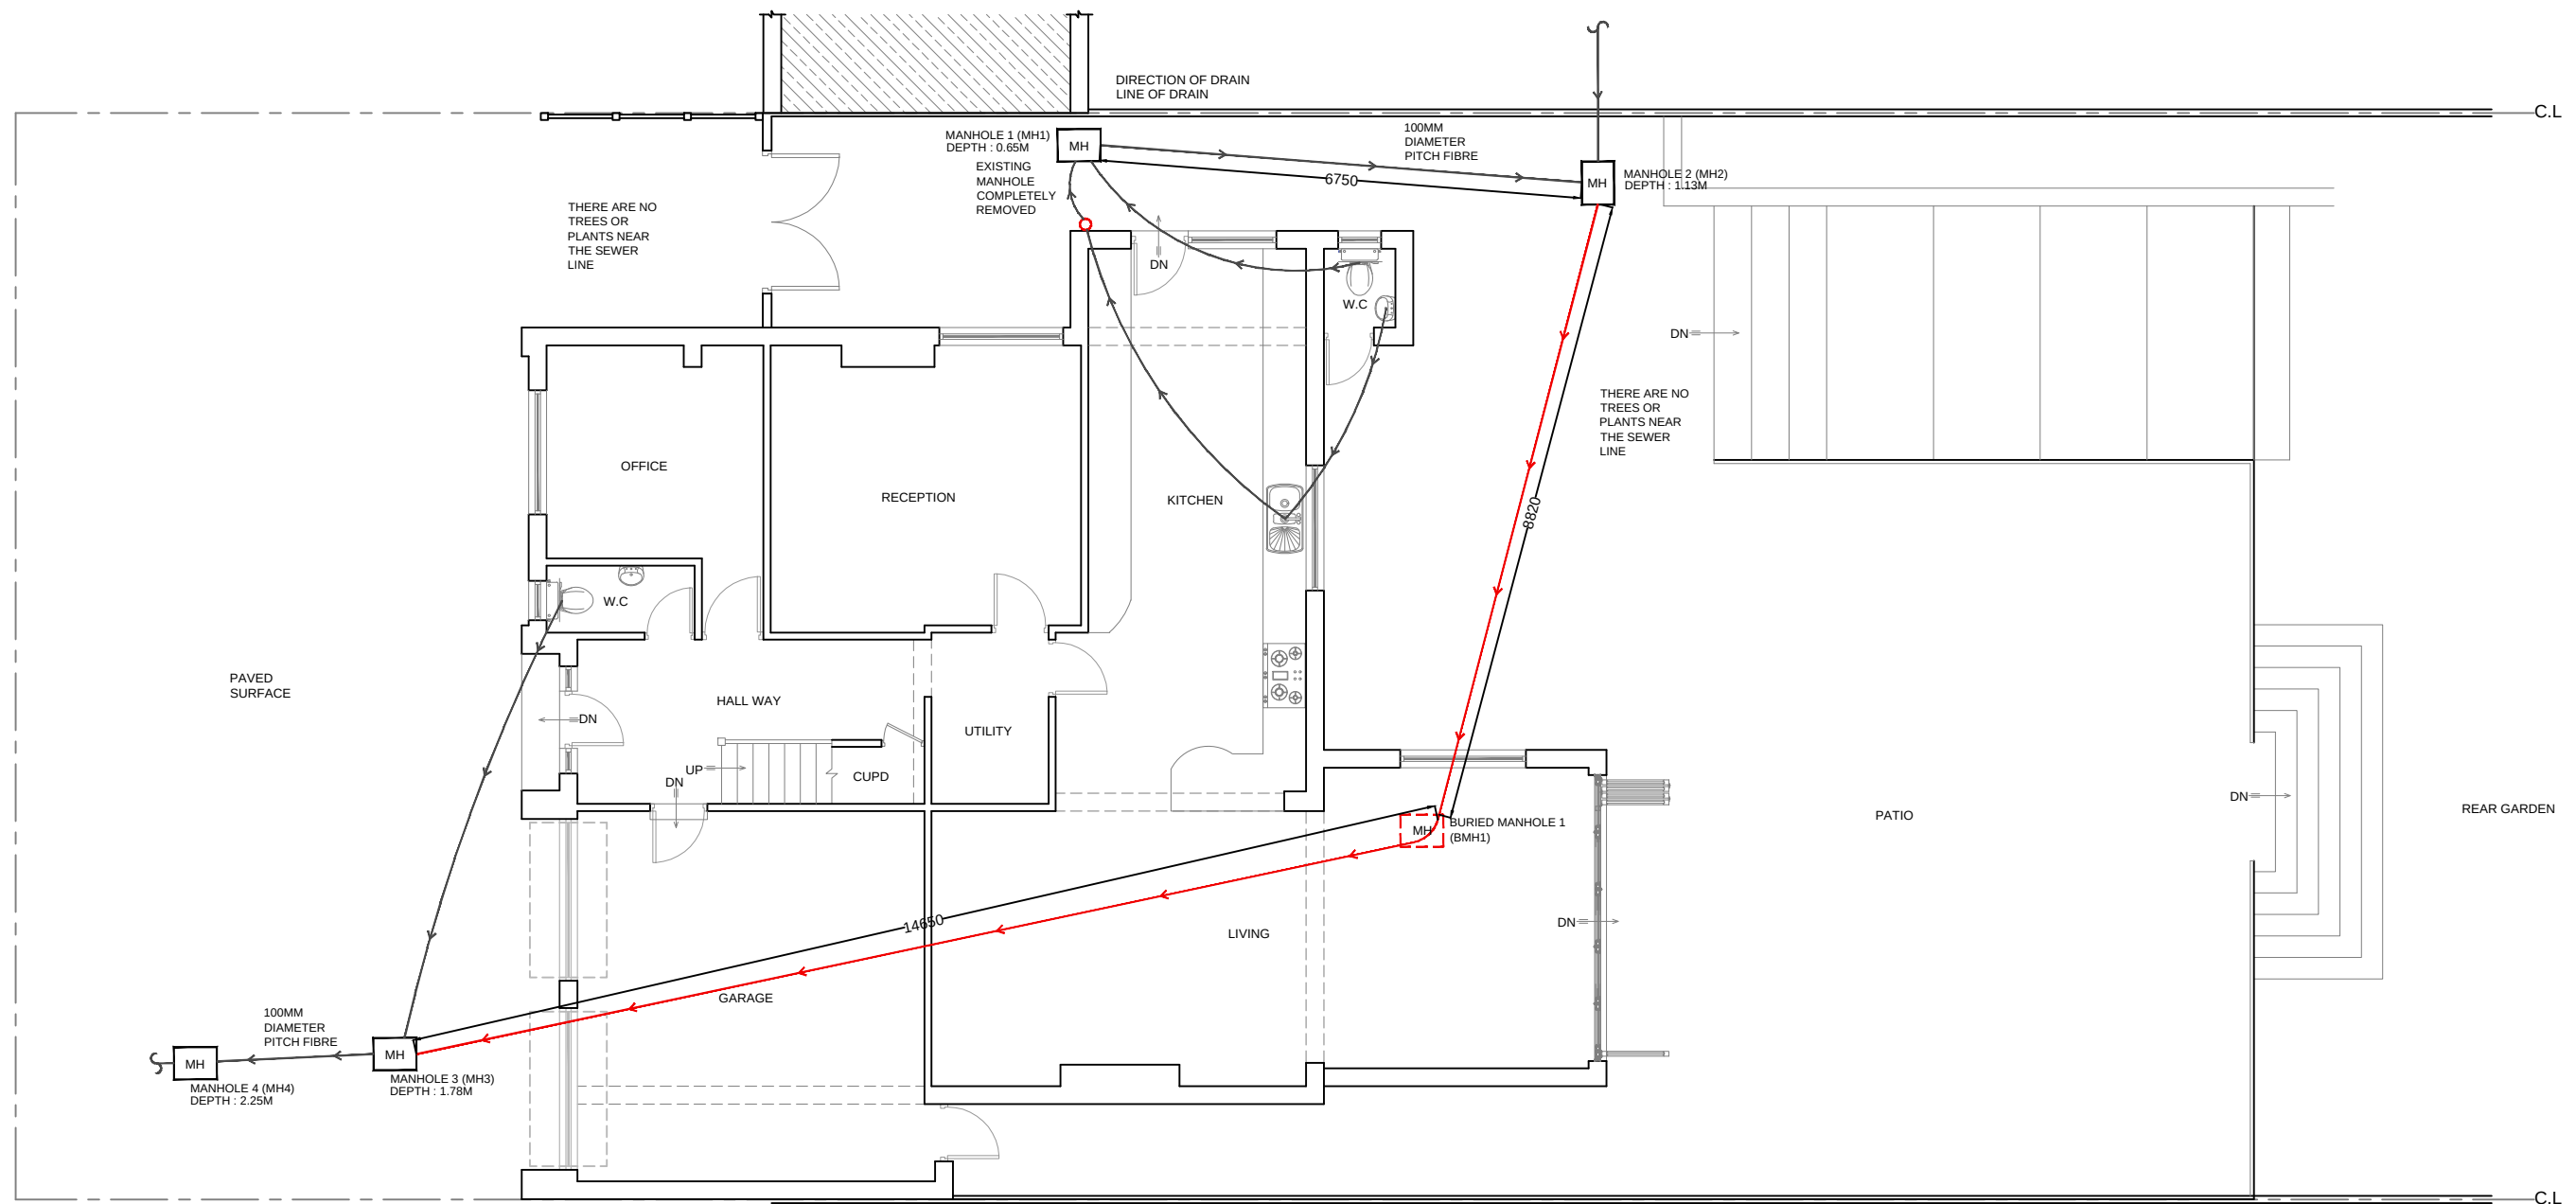

1:100
0 1 2 5 10 Meter

REFERENCE DRAWINGS

NOTES
PLEASE NOTE THAT BEFORE BUILDING WORKS COMMENCES IT IS
THE RESPONSIBILITY OF THE BUILDER OR OWNER TO SERVE PARTY
WALL NOTICES TO ALL NEIGHBORS

No	DATE	REVISION	BY	CHK

CONSULTANT



CIVIL ENGINEERS
STRUCTURAL ENGINEERS
ARCHITECTURAL DESIGNERS
Contact: 07947249323



DRAWN
F.R.
CHECKED
A.R.
PROJECT NO.

CLIENT/PROJECT

THE FENS CRAYS HILL
TITLE
EXISTING GROUND FLOOR PLAN

DRAWING No.


D01

SCALE: 1:100 @A3

DATE: 26-02-2024




EXISTING FIRST FLOOR PLAN

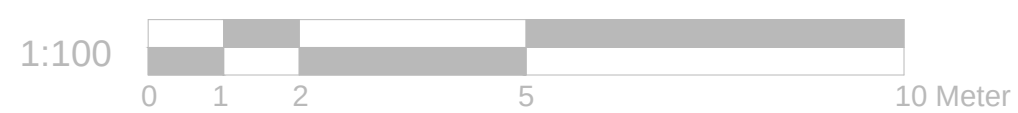


REFERENCE DRAWINGS		NOTES PLEASE NOTE THAT BEFORE BUILDING WORKS COMMENCES IT IS THE RESPONSIBILITY OF THE BUILDER OR OWNER TO SERVE PARTY WALL NOTICES TO ALL NEIGHBORS	No	DATE	REVISION	BY	CHK	CONSULTANT	DRAWN F.R	CLIENT/PROJECT	DRAWING No.
								 CIVIL ENGINEERS STRUCTURAL ENGINEERS ARCHITECTURAL DESIGNERS Contact: 07947249323	CHECKED A.R	THE FENS CRAYS HILL	D02
									PROJECT NO.		SCALE: 1:100 @A3
											DATE: 04-11-2023



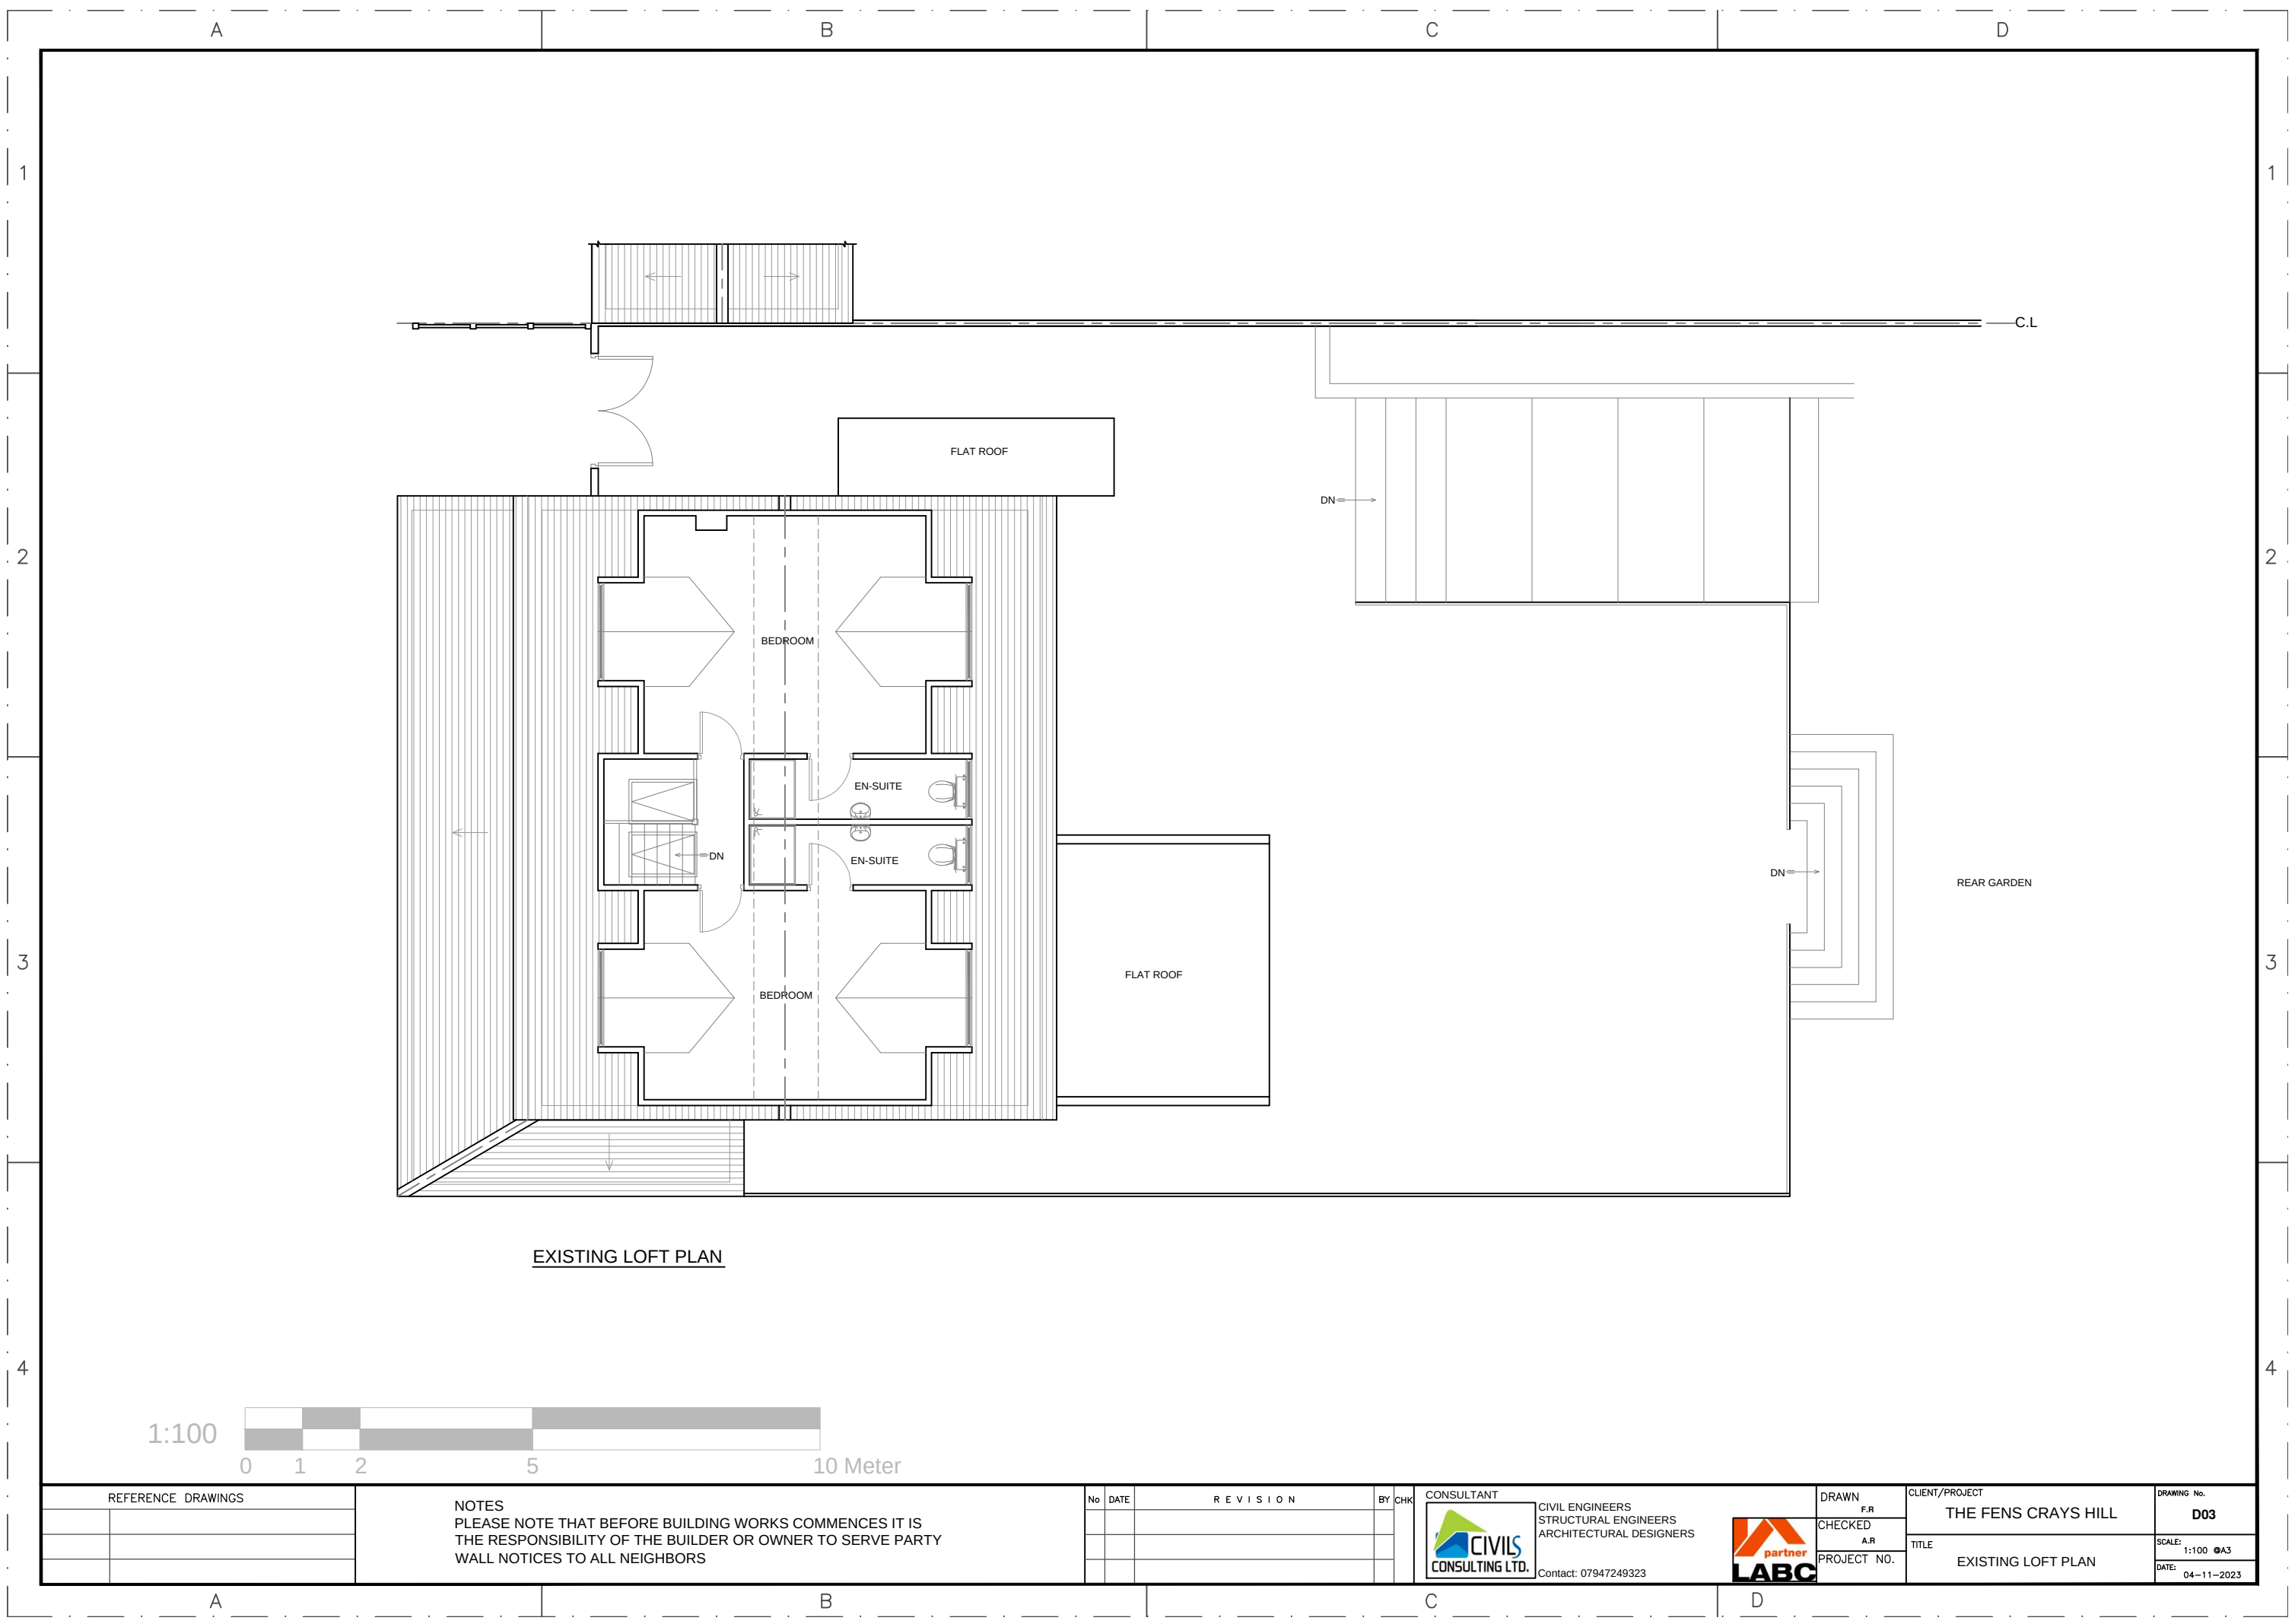

EXISTING LOFT PLAN

1:100

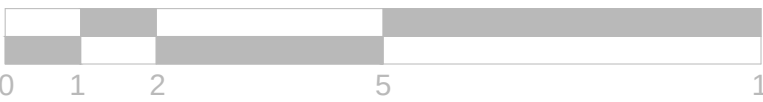

10 Meter

REFERENCE DRAWINGS	

NOTES
PLEASE NOTE THAT BEFORE BUILDING WORKS COMMENCES IT IS
THE RESPONSIBILITY OF THE BUILDER OR OWNER TO SERVE PARTY
WALL NOTICES TO ALL NEIGHBORS

No	DATE	REVISION	BY	CHK


CONSULTANT
**CIVILS**
CONSULTING LTD.
CIVIL ENGINEERS
STRUCTURAL ENGINEERS
ARCHITECTURAL DESIGNERS
Contact: 07947249323



DRAWN F.R
CHECKED A.R
PROJECT NO.


CLIENT/PROJECT	
THE FENS CRAYS HILL	
TITLE	EXISTING LOFT PLAN

DRAWING No.	D03
SCALE:	1:100 @A3
DATE:	04-11-2023

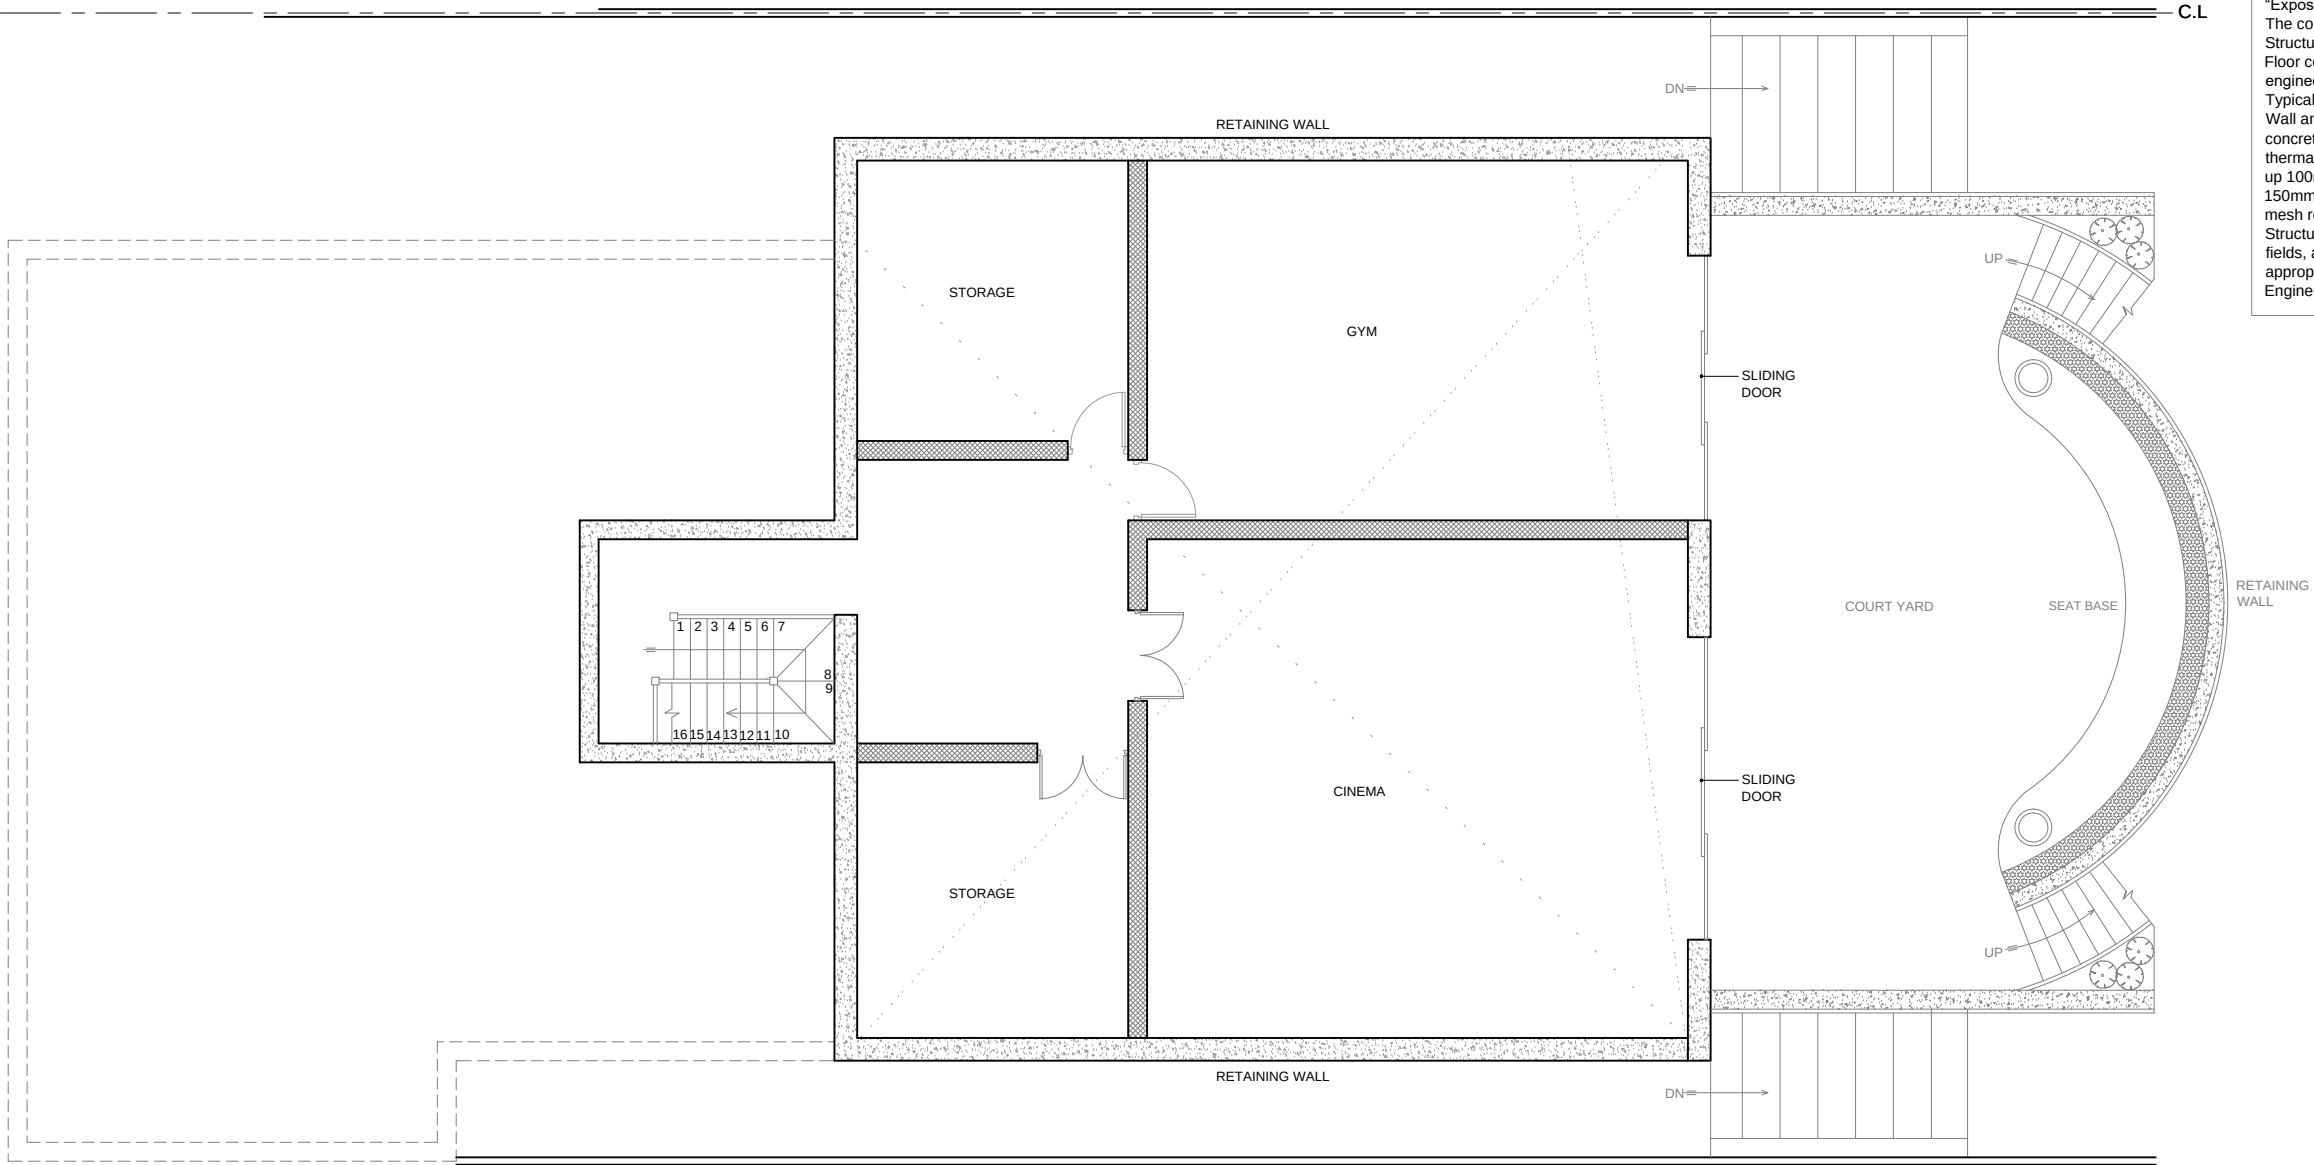


TYPE B STRUCTURALLY INTEGRAL PROTECTION (WATERPROOF CONCRETE)
Type B waterproofing to be designed and constructed in reinforced or prestressed concrete in accordance with BS EN 1992-1-1 and BS EN 1992-3 or MPA publication 'Concrete basements a Guidance on the design and construction of in-situ concrete basement structures'. Reference - Chapter 2.1 'Concrete and its reinforcement's'; or to BS EN 1992 part 3 and installed in accordance with the design by suitably experienced and trained operatives. Cement type and content to comply with BS EN 8500:2012 with respect to the "Exposure Class" for the specific conditions to be encountered. The compressive strength requirement to comply with the requirements of the Structural Engineer.
Floor construction design and wall insulation to be compatible with structural engineer's and concrete manufacturer's details.
Typical floor construction would be:
Wall and floor insulation to be 100mm Celotex GA4000 over waterproof concrete. 25mm insulation to continue around floor perimeters to avoid thermal bridging. A VCL should be laid over the insulation boards and turned up 100mm at room perimeters behind the skirting, all joints to be lapped 150mm and sealed. Finish with 65mm sand/cement finishing screed with light mesh reinforcement.
Structural waterproofing design and geotechnical investigations are specialist fields, advice must be sought from suitably experienced parties. An appropriate structural design must be undertaken by a Chartered Structural Engineer and waterproofing concrete specialist.

PROPOSED BASEMENT PLAN

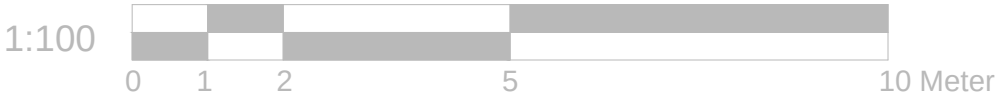


REFERENCE DRAWINGS		NOTES PLEASE NOTE THAT BEFORE BUILDING WORKS COMMENCES IT IS THE RESPONSIBILITY OF THE BUILDER OR OWNER TO SERVE PARTY WALL NOTICES TO ALL NEIGHBORS	No	DATE	REVISION	BY	CHK	CONSULTANT	DRAWN F.R	CLIENT/PROJECT		DRAWING No.
								CIVIL ENGINEERS STRUCTURAL ENGINEERS ARCHITECTURAL DESIGNERS Contact: 07947249323 	CHECKED A.R	THE FENS CRAYS HILL		D04
									PROJECT NO.	PROPOSED BASMENT PLAN		SCALE: 1:100 @A3
												DATE: 04-11-2023

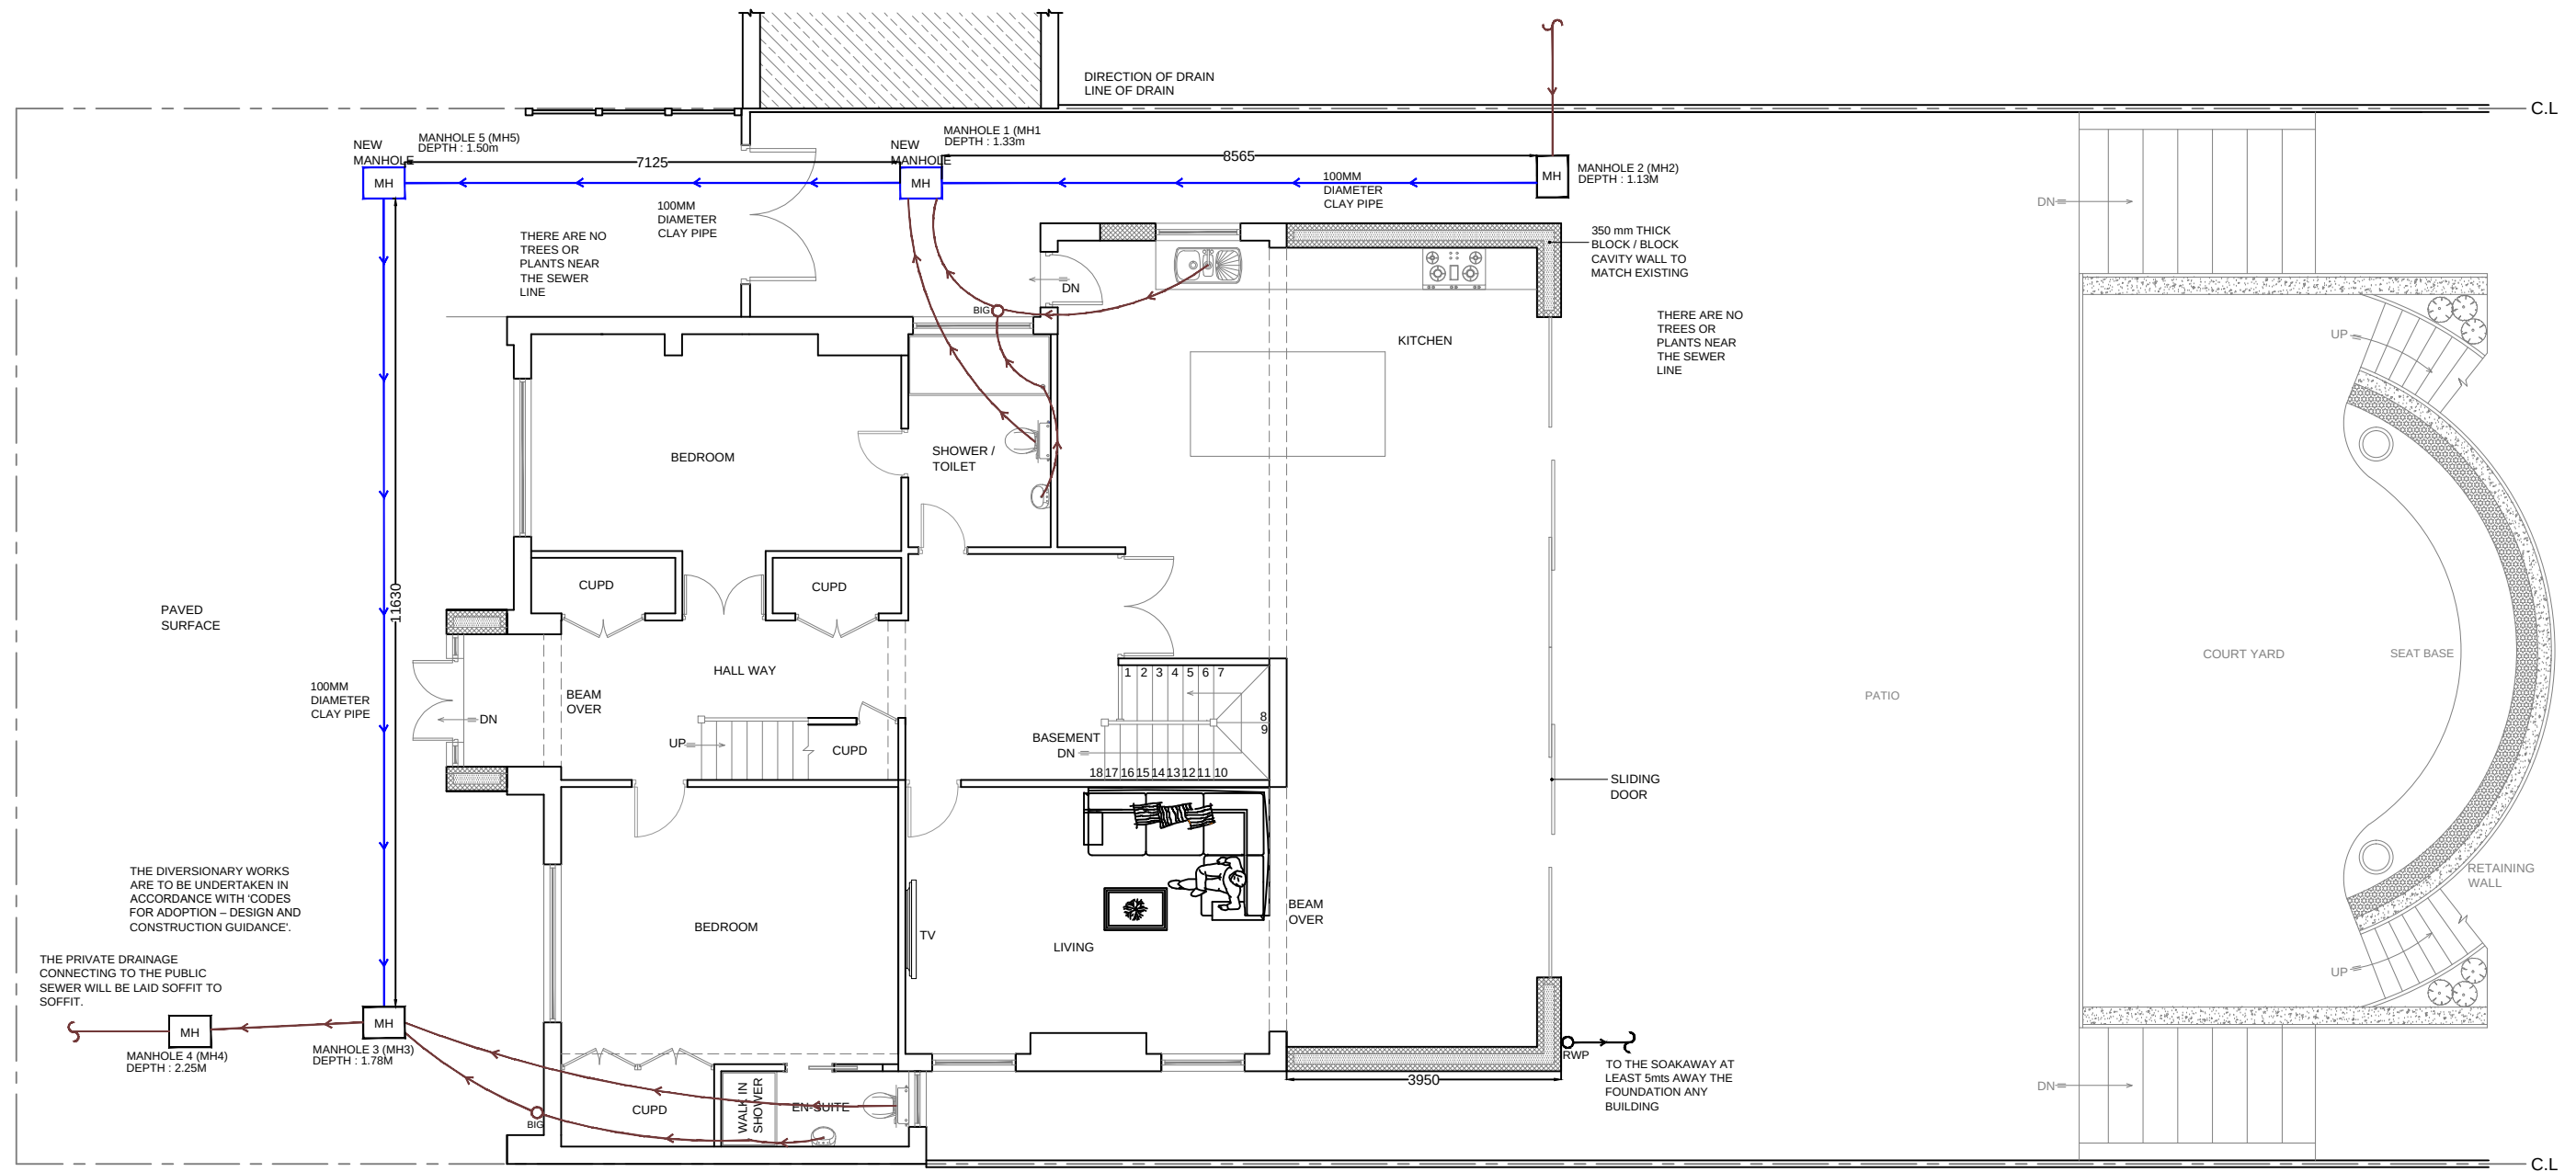

PROPOSED GROUND FLOOR PLAN

1:100

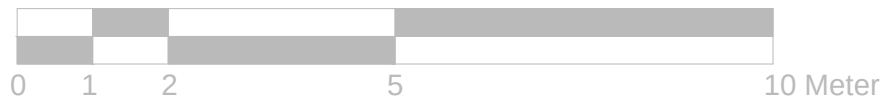

REFERENCE DRAWINGS

NOTES

PLEASE NOTE THAT BEFORE BUILDING WORKS COMMENCES IT IS THE RESPONSIBILITY OF THE BUILDER OR OWNER TO SERVE PARTY WALL NOTICES TO ALL NEIGHBORS

No	DATE	REVISION	BY	CHK

CONSULTANT



CIVIL ENGINEERS
STRUCTURAL ENGINEERS
ARCHITECTURAL DESIGNERS
Contact: 07947249323



DRAWN F.R.
CHECKED A.R.
PROJECT NO.

CLIENT/PROJECT

THE FENS CRAYS HILL

TITLE


PROPOSED GROUND FLOOR PLAN

DRAWING No.

D05


SCALE: 1:100 @A3

DATE: 26-02-2024

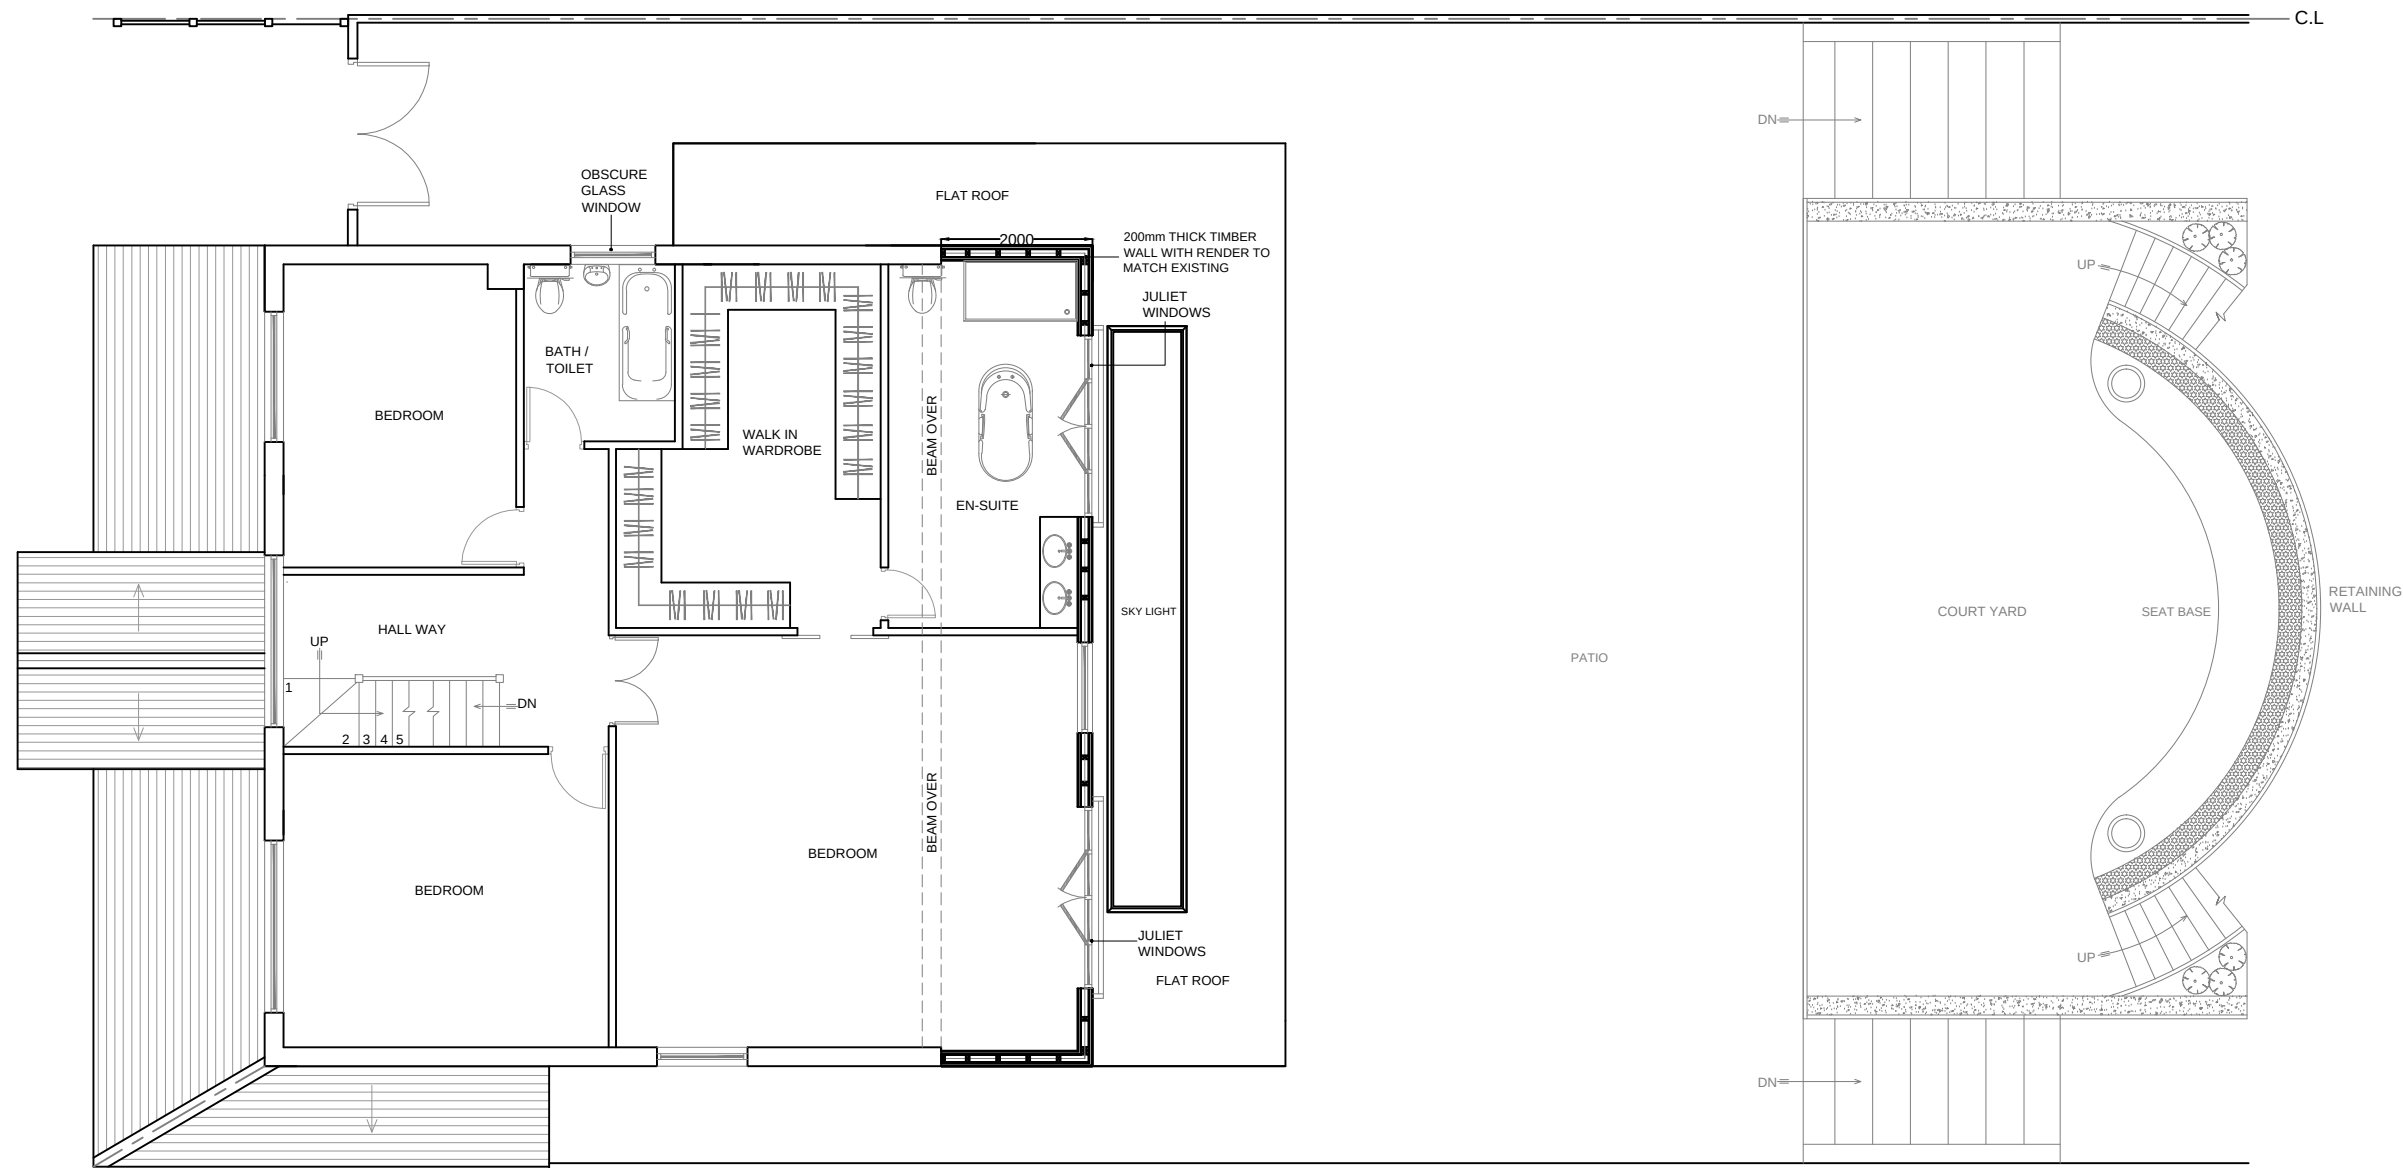

PROPOSED FIRST FLOOR PLAN

1:100

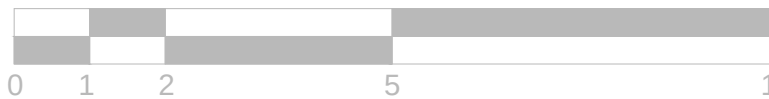

10 Meter

REFERENCE DRAWINGS	


NOTES
PLEASE NOTE THAT BEFORE BUILDING WORKS COMMENCES IT IS
THE RESPONSIBILITY OF THE BUILDER OR OWNER TO SERVE PARTY
WALL NOTICES TO ALL NEIGHBORS


No	DATE	REVISION	BY	CHK

CONSULTANT	
	CIVIL ENGINEERS STRUCTURAL ENGINEERS ARCHITECTURAL DESIGNERS
	Contact: 07947249323




DRAWN		CLIENT/PROJECT	DRAWING No.
F.R			
CHECKED		THE FENS CRAYS HILL	D06
A.R			
PROJECT NO.		TITLE	SCALE: 1:100 @A3
		PROPOSED FIRST FLOOR PLAN	DATE: 04-11-2023

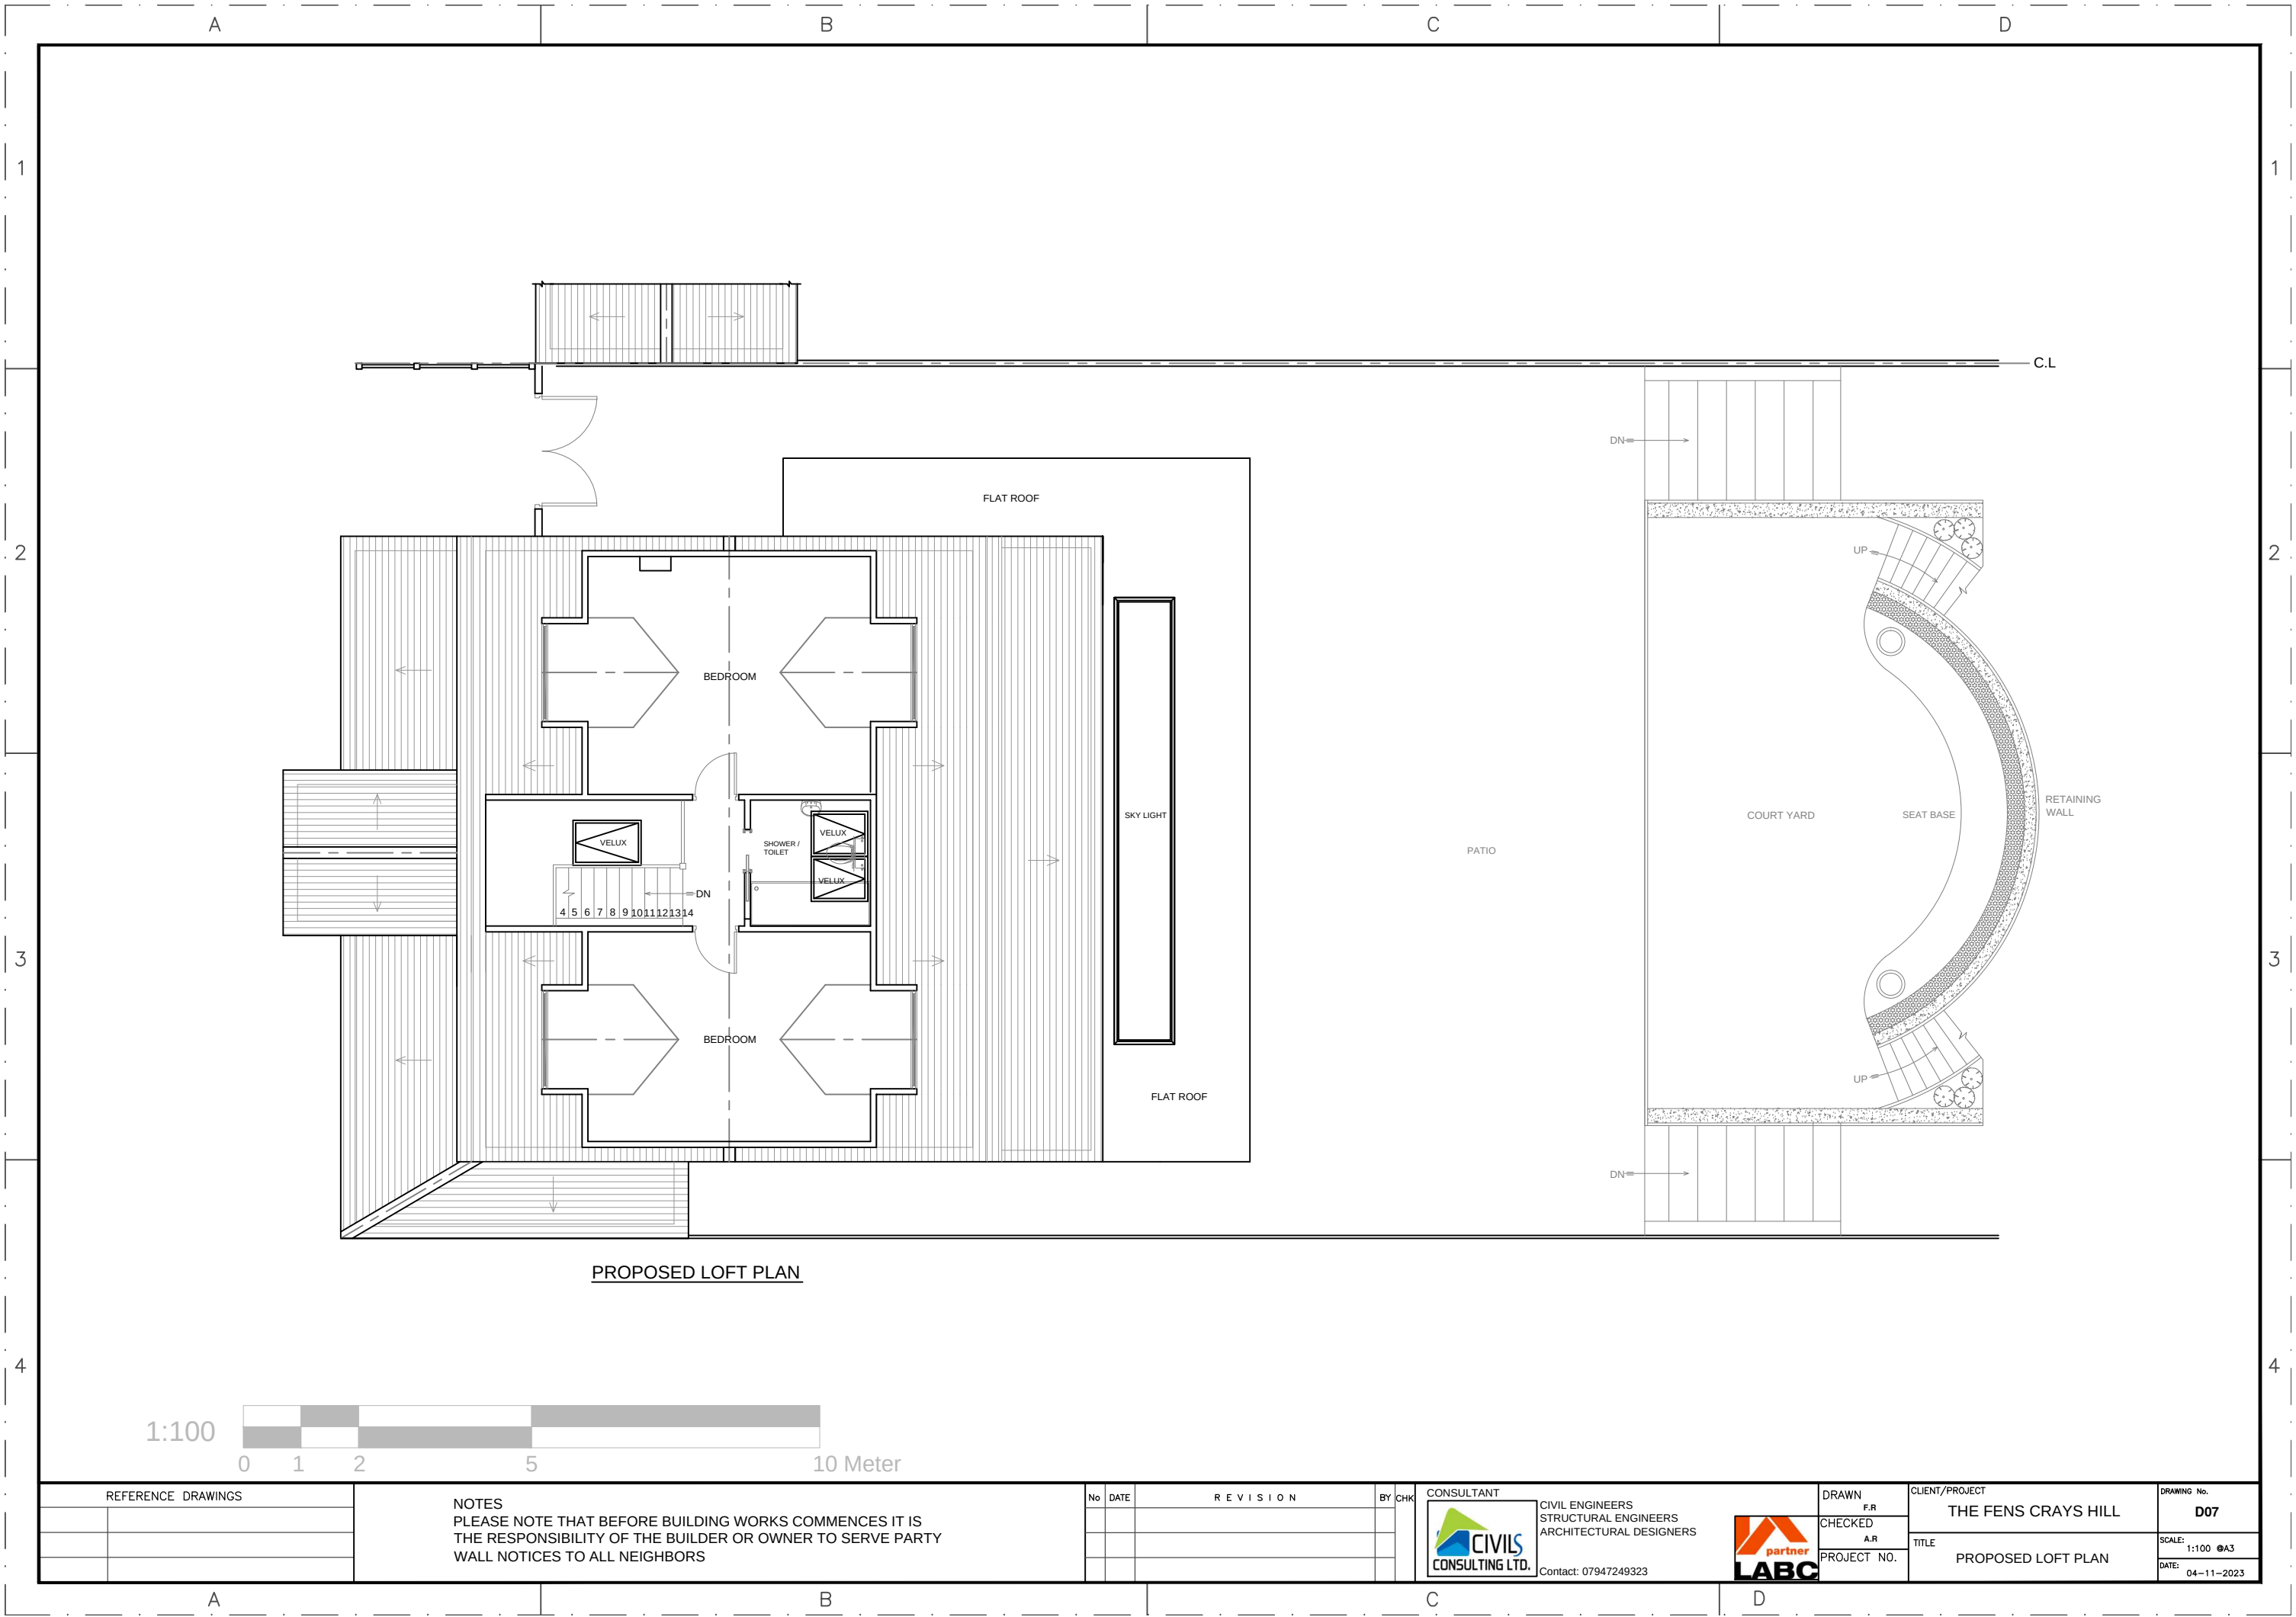

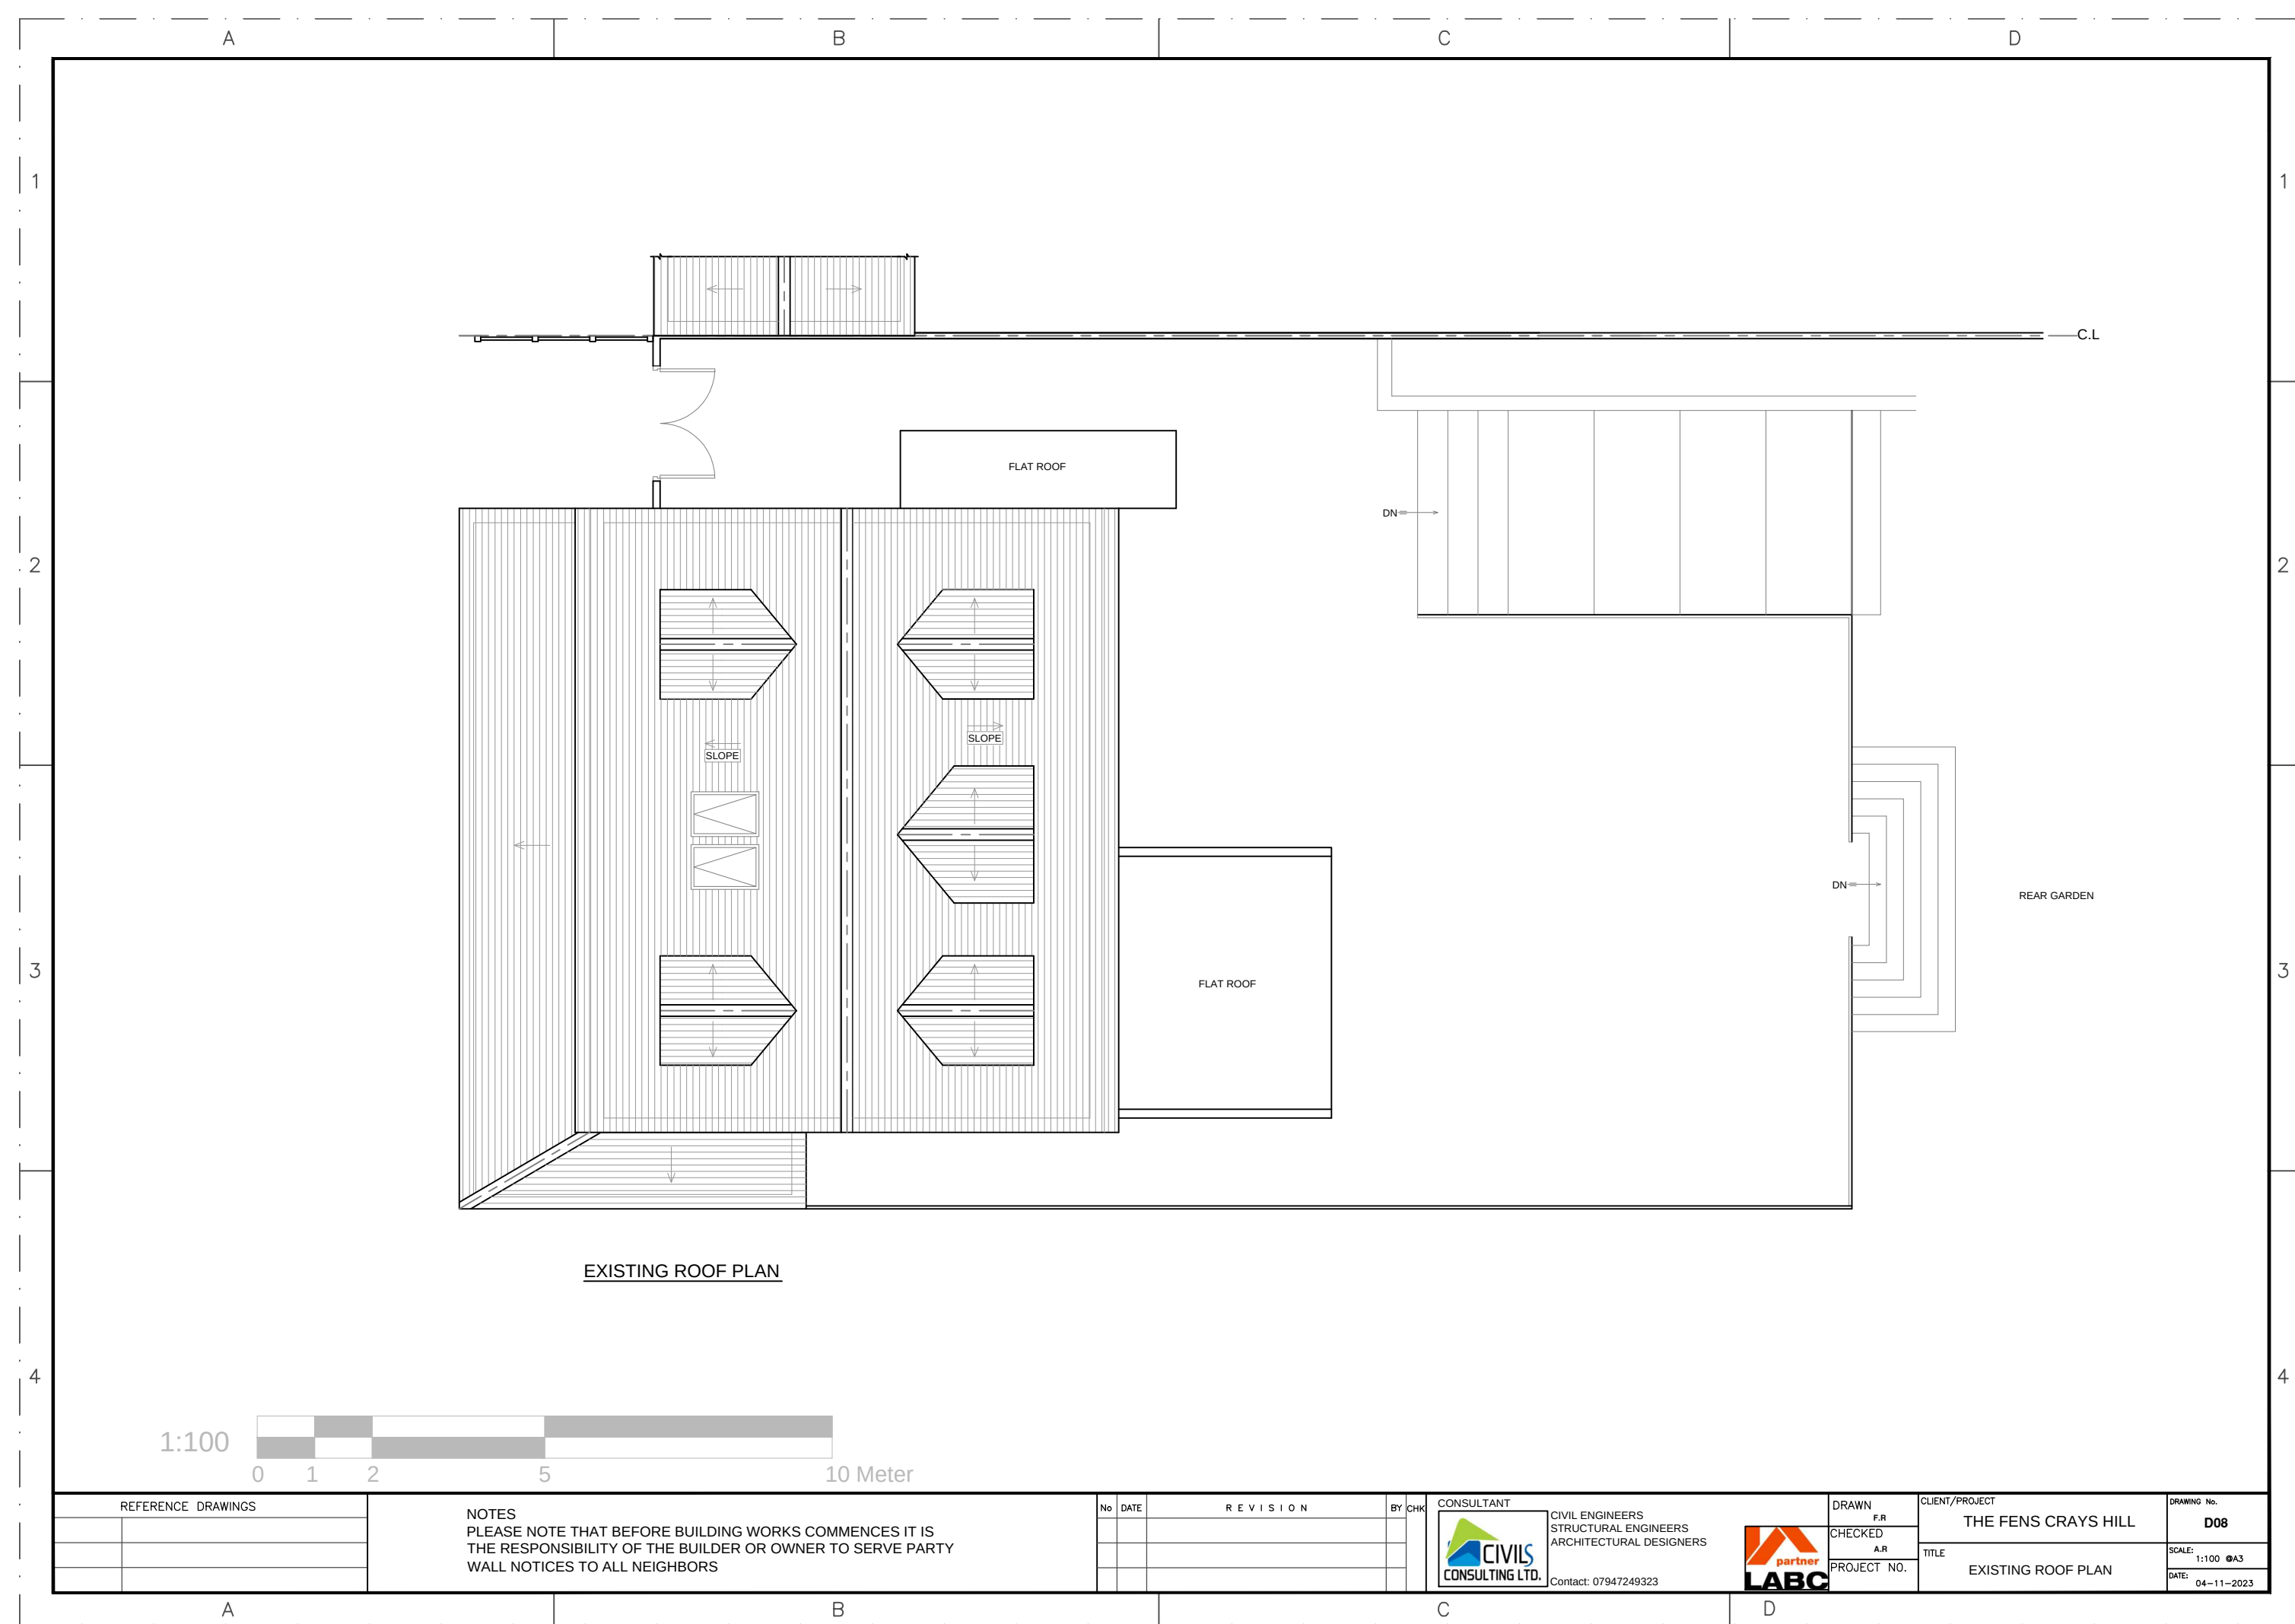

EXISTING ROOF PLAN

1:100

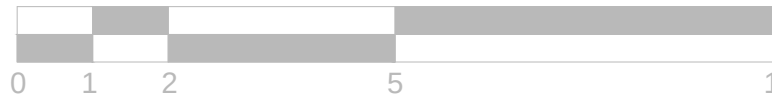

10 Meter

REFERENCE DRAWINGS

NOTES

PLEASE NOTE THAT BEFORE BUILDING WORKS COMMENCES IT IS THE RESPONSIBILITY OF THE BUILDER OR OWNER TO SERVE PARTY WALL NOTICES TO ALL NEIGHBORS

No	DATE	REVISION	BY	CHK

CONSULTANT



CIVIL ENGINEERS
STRUCTURAL ENGINEERS
ARCHITECTURAL DESIGNERS
Contact: 07947249323



DRAWN F.R
CHECKED A.R
PROJECT NO.

CLIENT/PROJECT


THE FENS CRAYS HILL
TITLE
EXISTING ROOF PLAN

DRAWING No.

D08


SCALE: 1:100 @A3

DATE: 04-11-2023

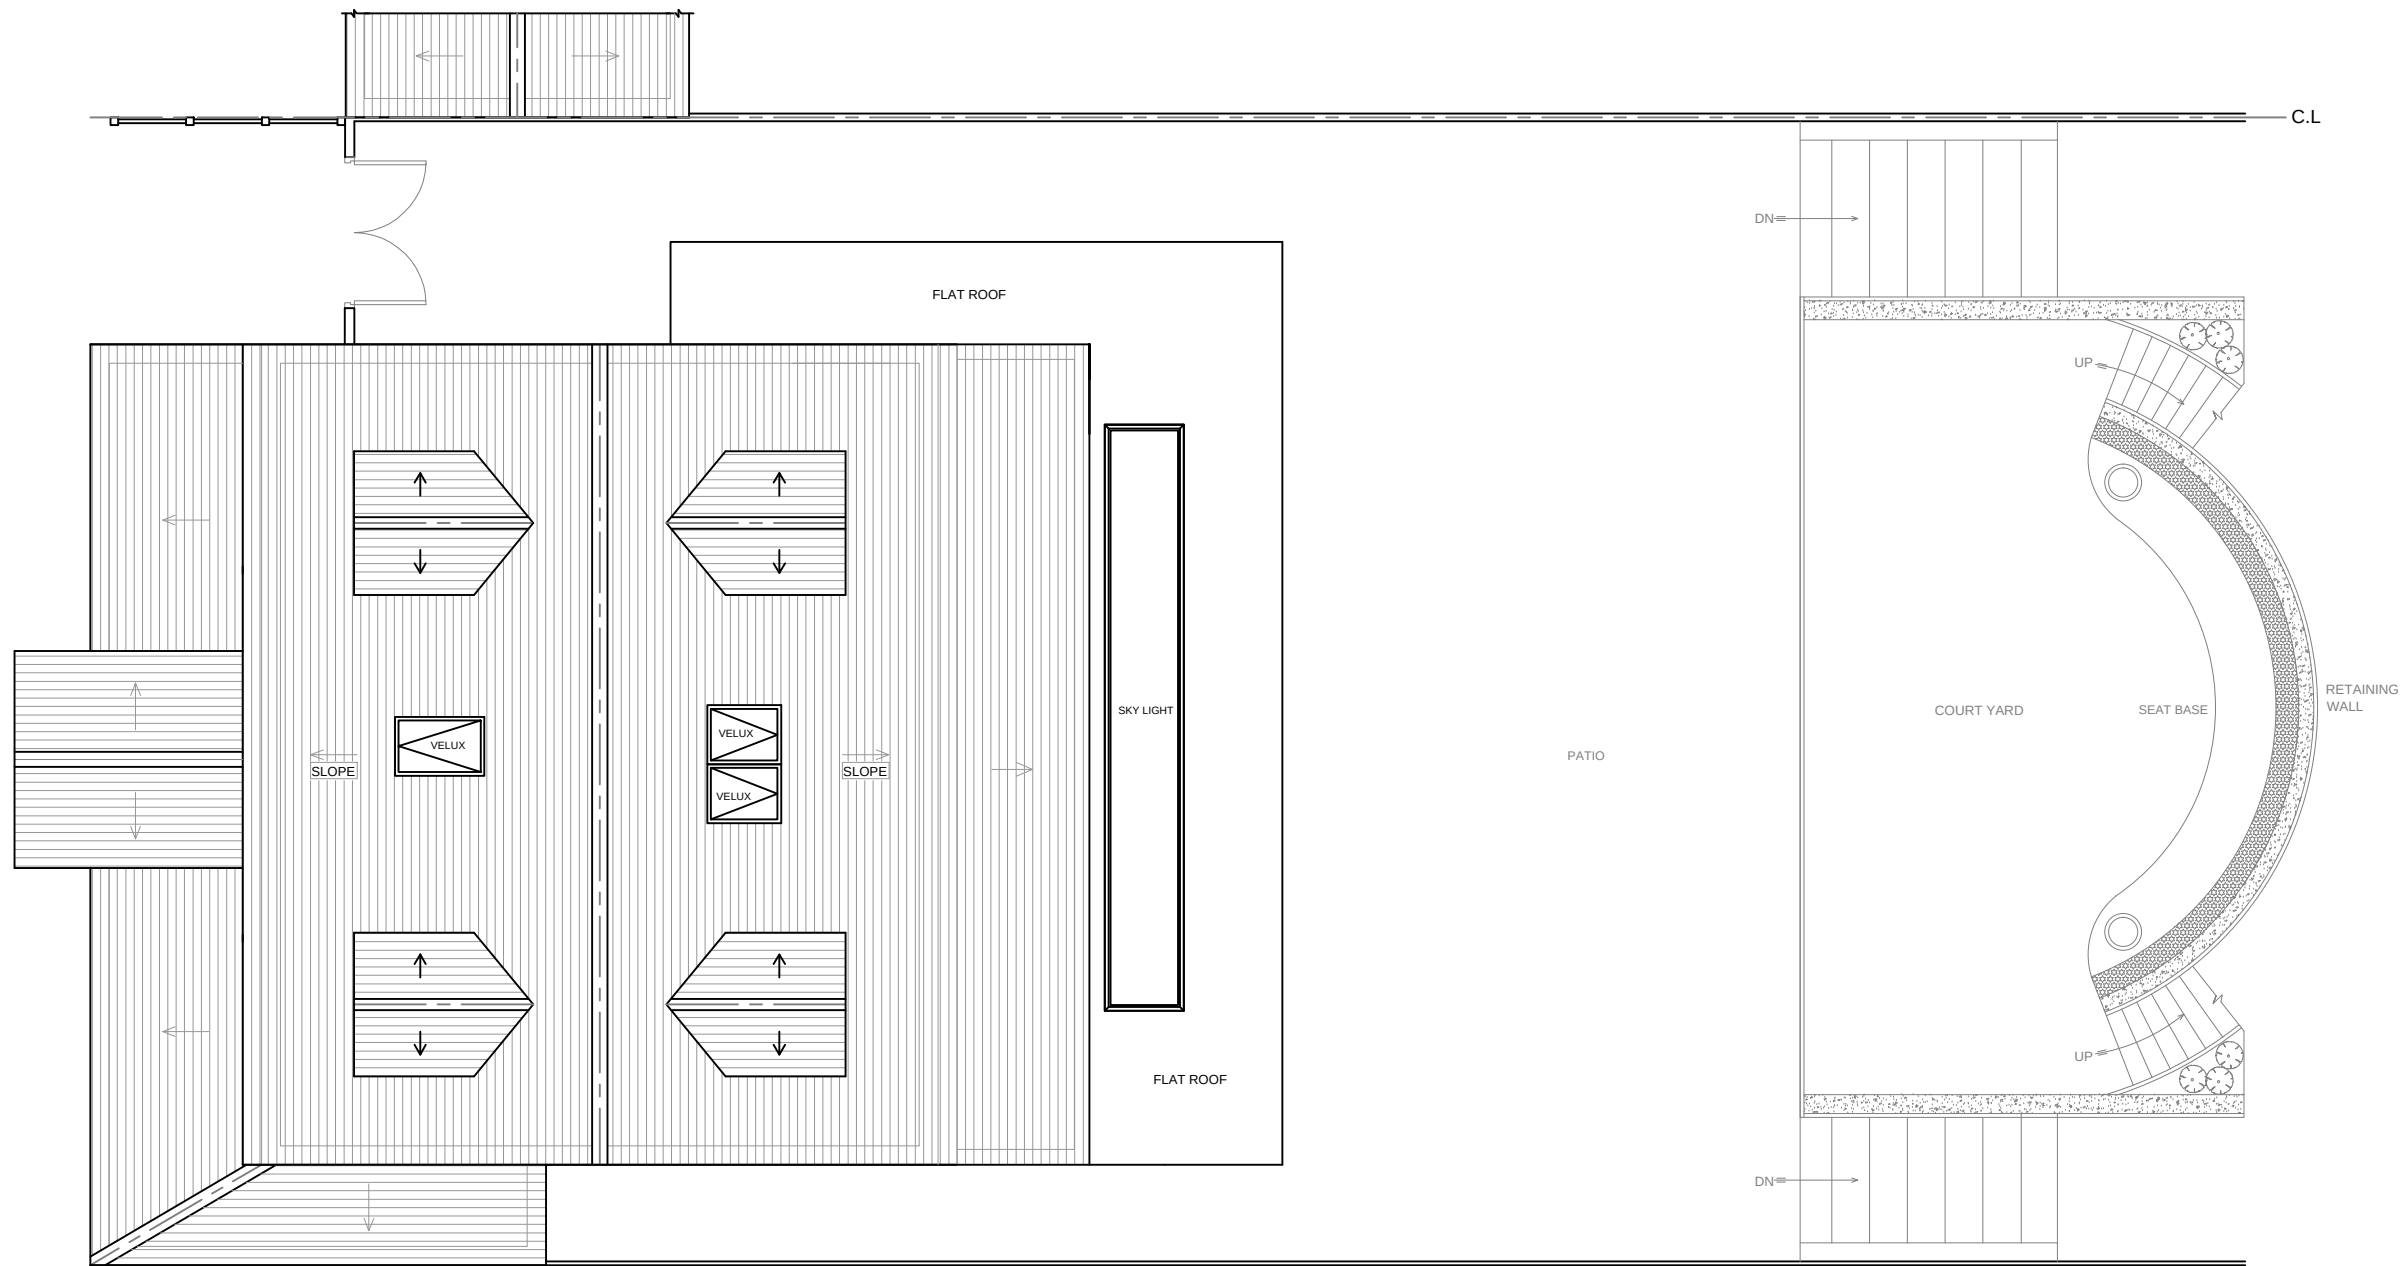

PROPOSED ROOF PLAN

1:100

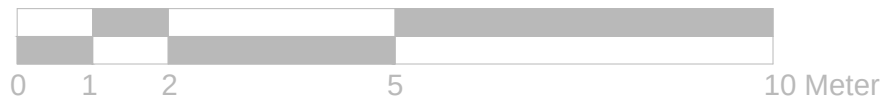

REFERENCE DRAWINGS

NOTES
PLEASE NOTE THAT BEFORE BUILDING WORKS COMMENCES IT IS
THE RESPONSIBILITY OF THE BUILDER OR OWNER TO SERVE PARTY
WALL NOTICES TO ALL NEIGHBORS

No	DATE	REVISION	BY	CHK

CONSULTANT



CIVIL ENGINEERS
STRUCTURAL ENGINEERS
ARCHITECTURAL DESIGNERS
Contact: 07947249323



DRAWN F.R
CHECKED A.R
PROJECT NO.

CLIENT/PROJECT THE FENS CRAYS HILL
TITLE PROPOSED ROOF PLAN

DRAWING No. D09
SCALE: 1:100 @A3
DATE: 04-11-2023

A

B

C

D

1

2

3

4

1

2

3

4



1:100
0 1 2 5 10 Meter

REFERENCE DRAWINGS

NOTES
PLEASE NOTE THAT BEFORE BUILDING WORKS COMMENCES IT IS
THE RESPONSIBILITY OF THE BUILDER OR OWNER TO SERVE PARTY
WALL NOTICES TO ALL NEIGHBORS

No	DATE	REVISION	BY	CHK

CONSULTANT

CIVIL ENGINEERS
STRUCTURAL ENGINEERS
ARCHITECTURAL DESIGNERS
Contact: 07947249323



DRAWN
F.R.
CHECKED
A.R.
PROJECT NO.

CLIENT/PROJECT
THE FENS CRAYS HILL
TITLE
EXISTING ELEVATIONS


DRAWING No.
D10
SCALE: 1:100 @A3
DATE: 04-11-2023

A

B

C

D

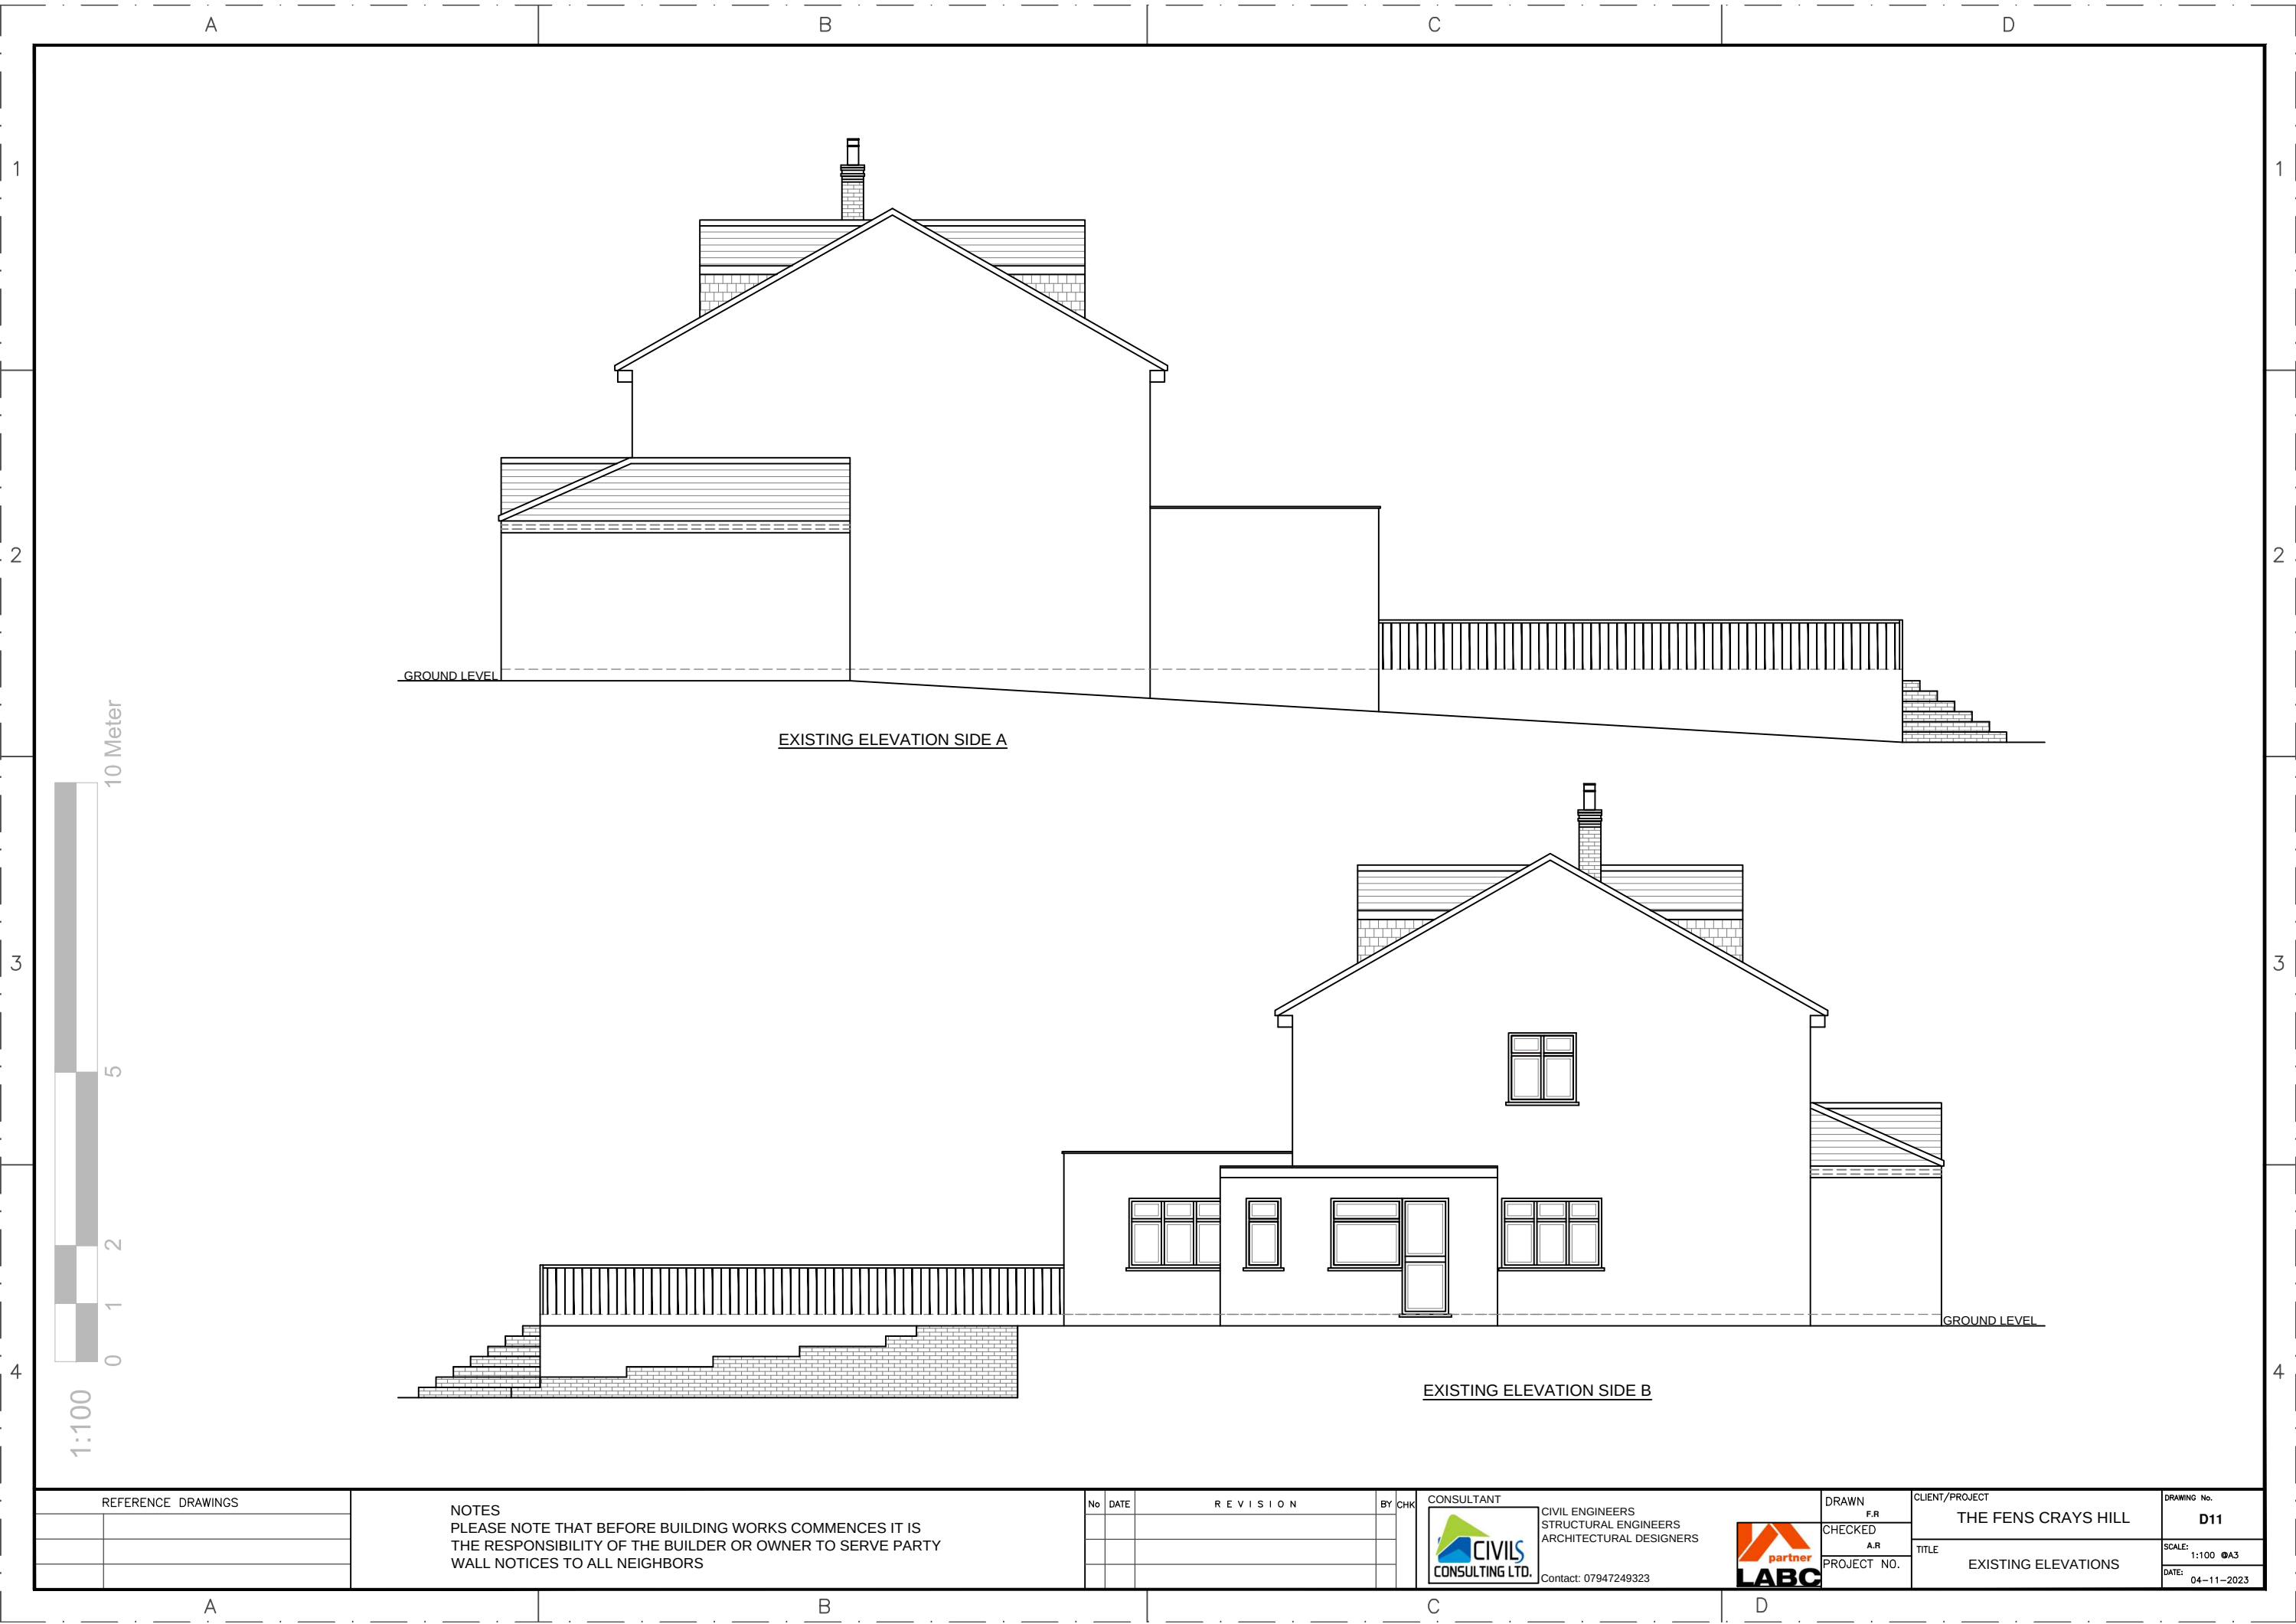

REFERENCE DRAWINGS	

NOTES
PLEASE NOTE THAT BEFORE BUILDING WORKS COMMENCES IT IS
THE RESPONSIBILITY OF THE BUILDER OR OWNER TO SERVE PARTY
WALL NOTICES TO ALL NEIGHBORS

No	DATE	REVISION	BY	CHK

CONSULTANT



CIVILS
CONSULTING LTD.

CIVIL ENGINEERS
STRUCTURAL ENGINEERS
ARCHITECTURAL DESIGNERS

Contact: 07947249323




DRAWN F.R	CLIENT/PROJECT THE FENS CRAYS HILL	DRAWING No. D11
CHECKED A.R		SCALE: 1:100 @A3
PROJECT NO.	TITLE EXISTING ELEVATIONS	DATE: 04-11-2023



REFERENCE DRAWINGS		NOTES PLEASE NOTE THAT BEFORE BUILDING WORKS COMMENCES IT IS THE RESPONSIBILITY OF THE BUILDER OR OWNER TO SERVE PARTY WALL NOTICES TO ALL NEIGHBORS	No		DATE	REVISION		BY	CHK	CONSULTANT CIVIL ENGINEERS STRUCTURAL ENGINEERS ARCHITECTURAL DESIGNERS Contact: 07947249323	DRAWN F.R. CHECKED A.R. PROJECT NO.	CLIENT/PROJECT THE FENS CRAYS HILL TITLE PROPOSED ELEVATIONS	DRAWING No. D12 SCALE: 1:100 @A3 DATE: 04-11-2023



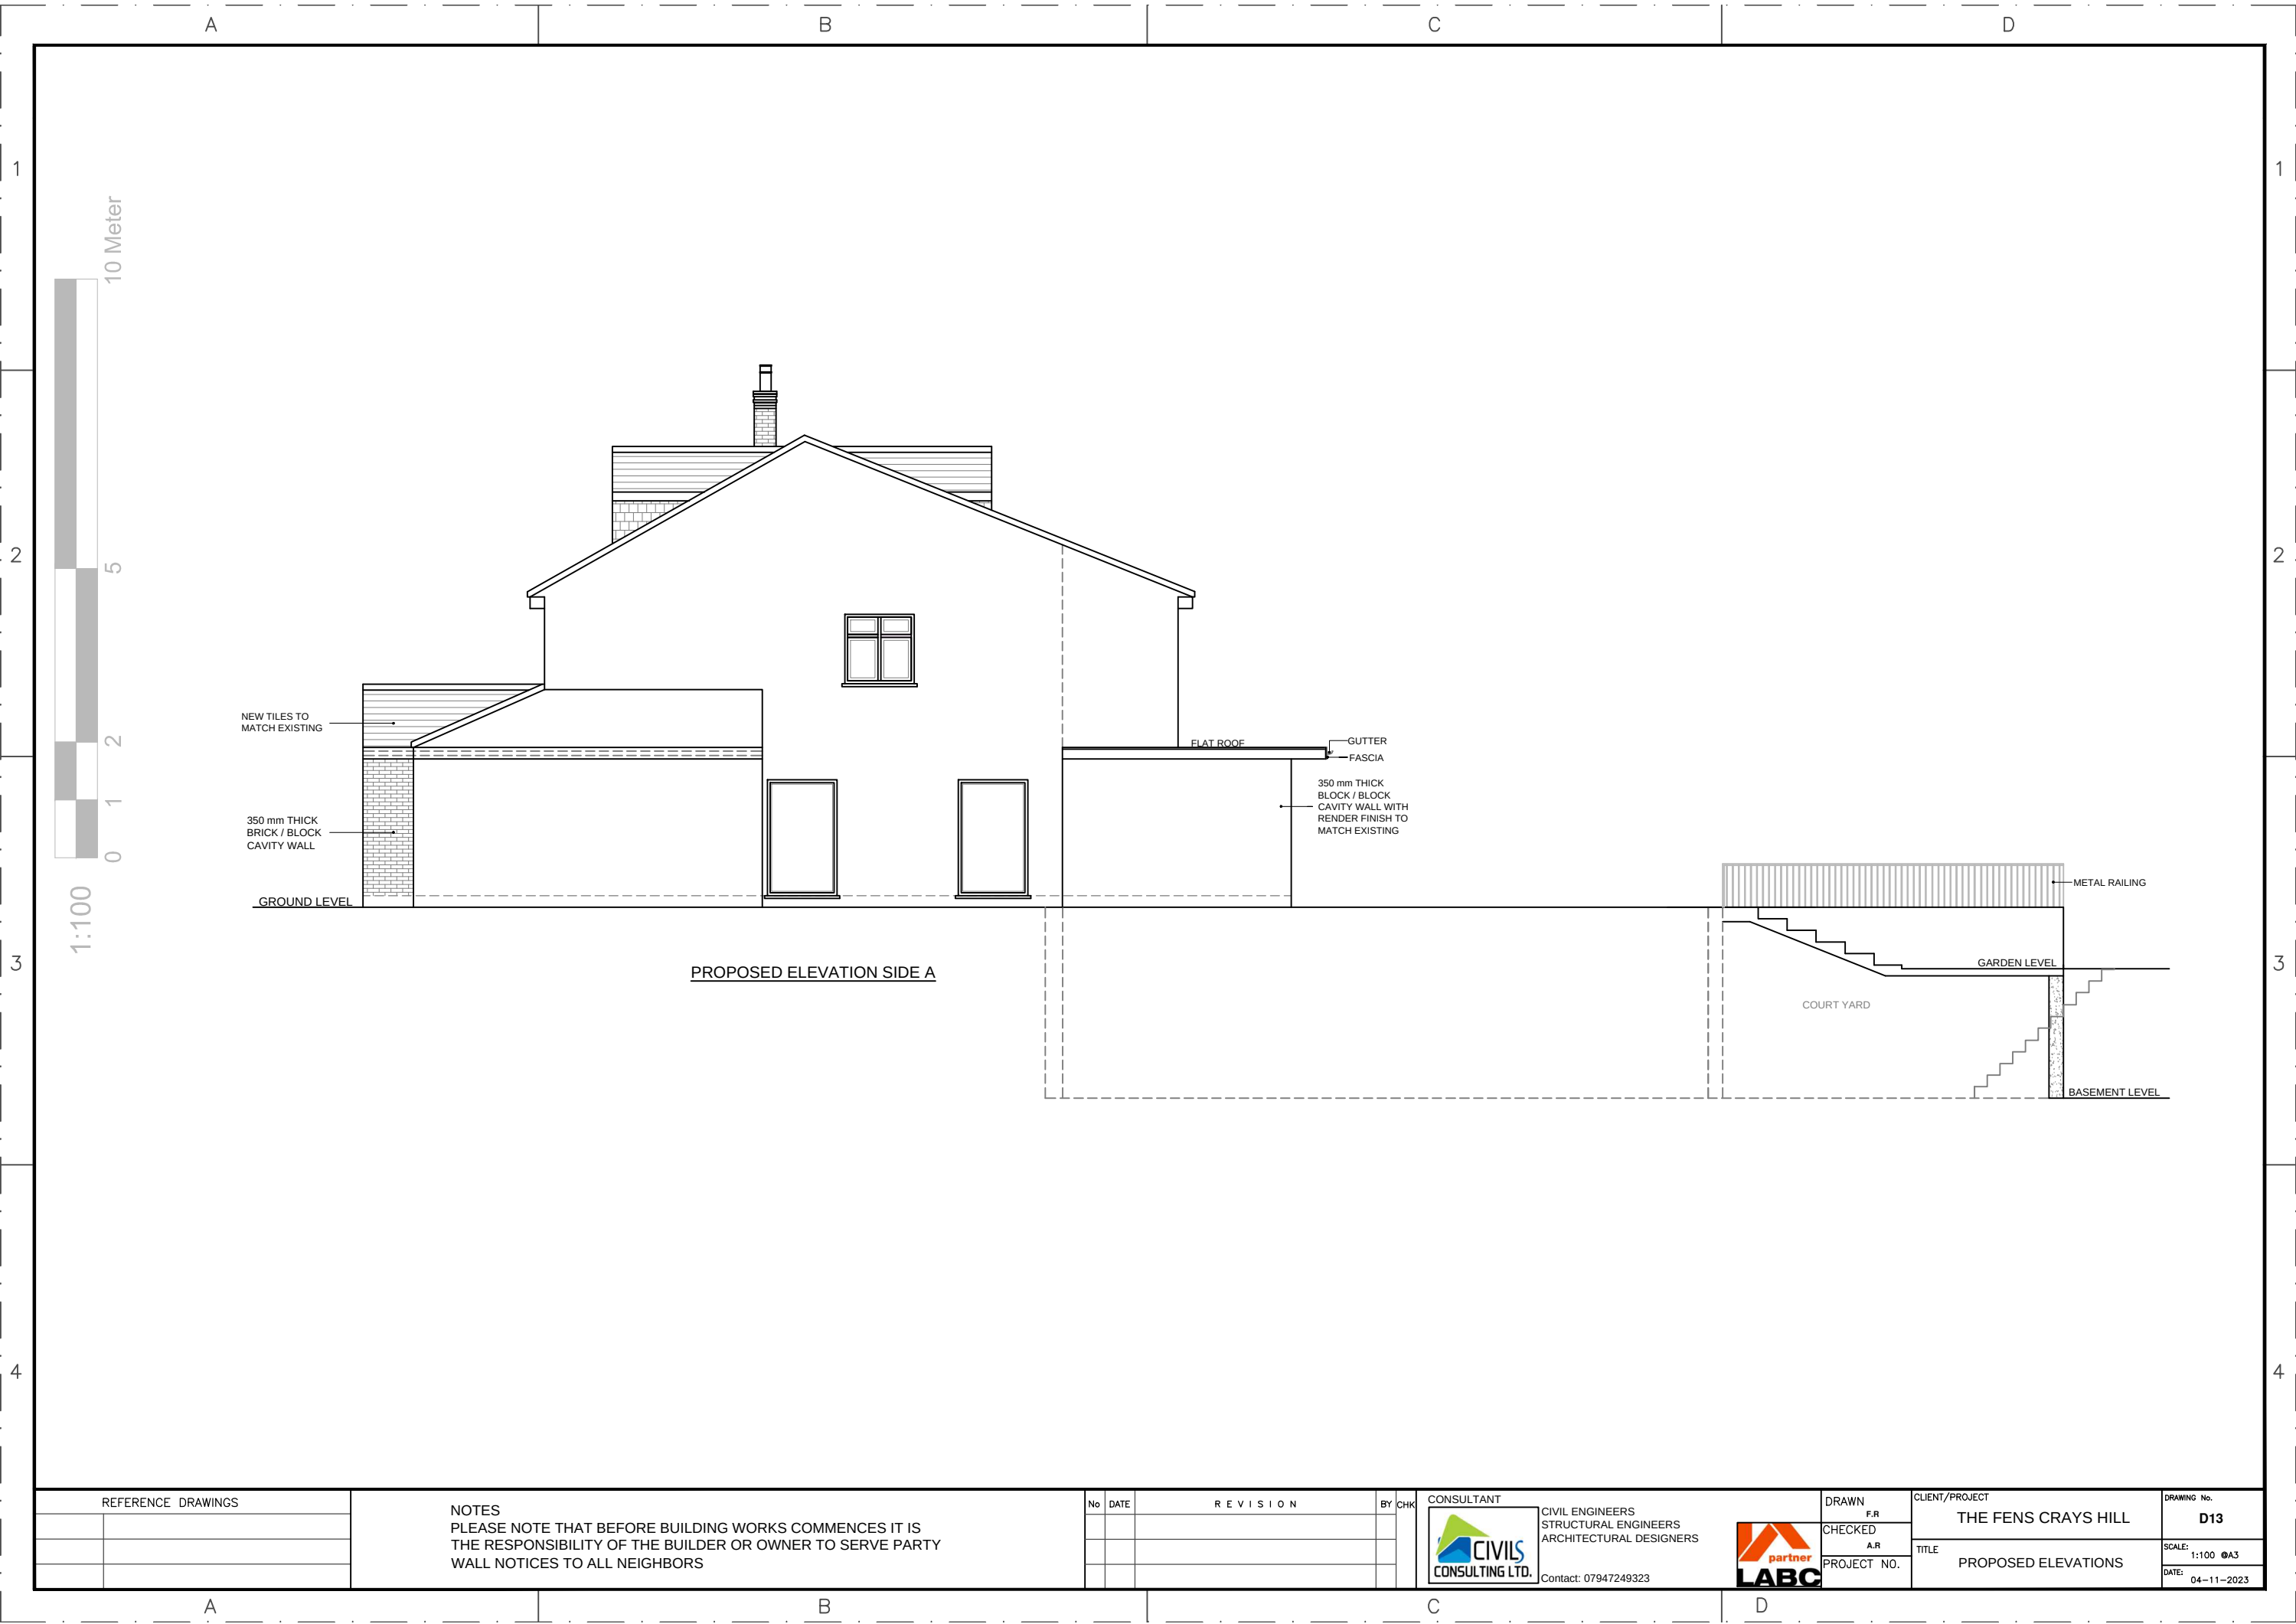

REFERENCE DRAWINGS	

NOTES
PLEASE NOTE THAT BEFORE BUILDING WORKS COMMENCES IT IS
THE RESPONSIBILITY OF THE BUILDER OR OWNER TO SERVE PARTY
WALL NOTICES TO ALL NEIGHBORS

No	DATE	REVISION	BY	CHK

CONSULTANT

**CIVILS**
CONSULTING LTD.


CIVIL ENGINEERS
STRUCTURAL ENGINEERS
ARCHITECTURAL DESIGNERS
Contact: 07947249323



DRAWN F.R
CHECKED A.R
PROJECT NO.

CLIENT/PROJECT	
THE FENS CRAYS HILL	
TITLE	PROPOSED ELEVATIONS

DRAWING No.	D13
SCALE:	1:100 @A3
DATE:	04-11-2023

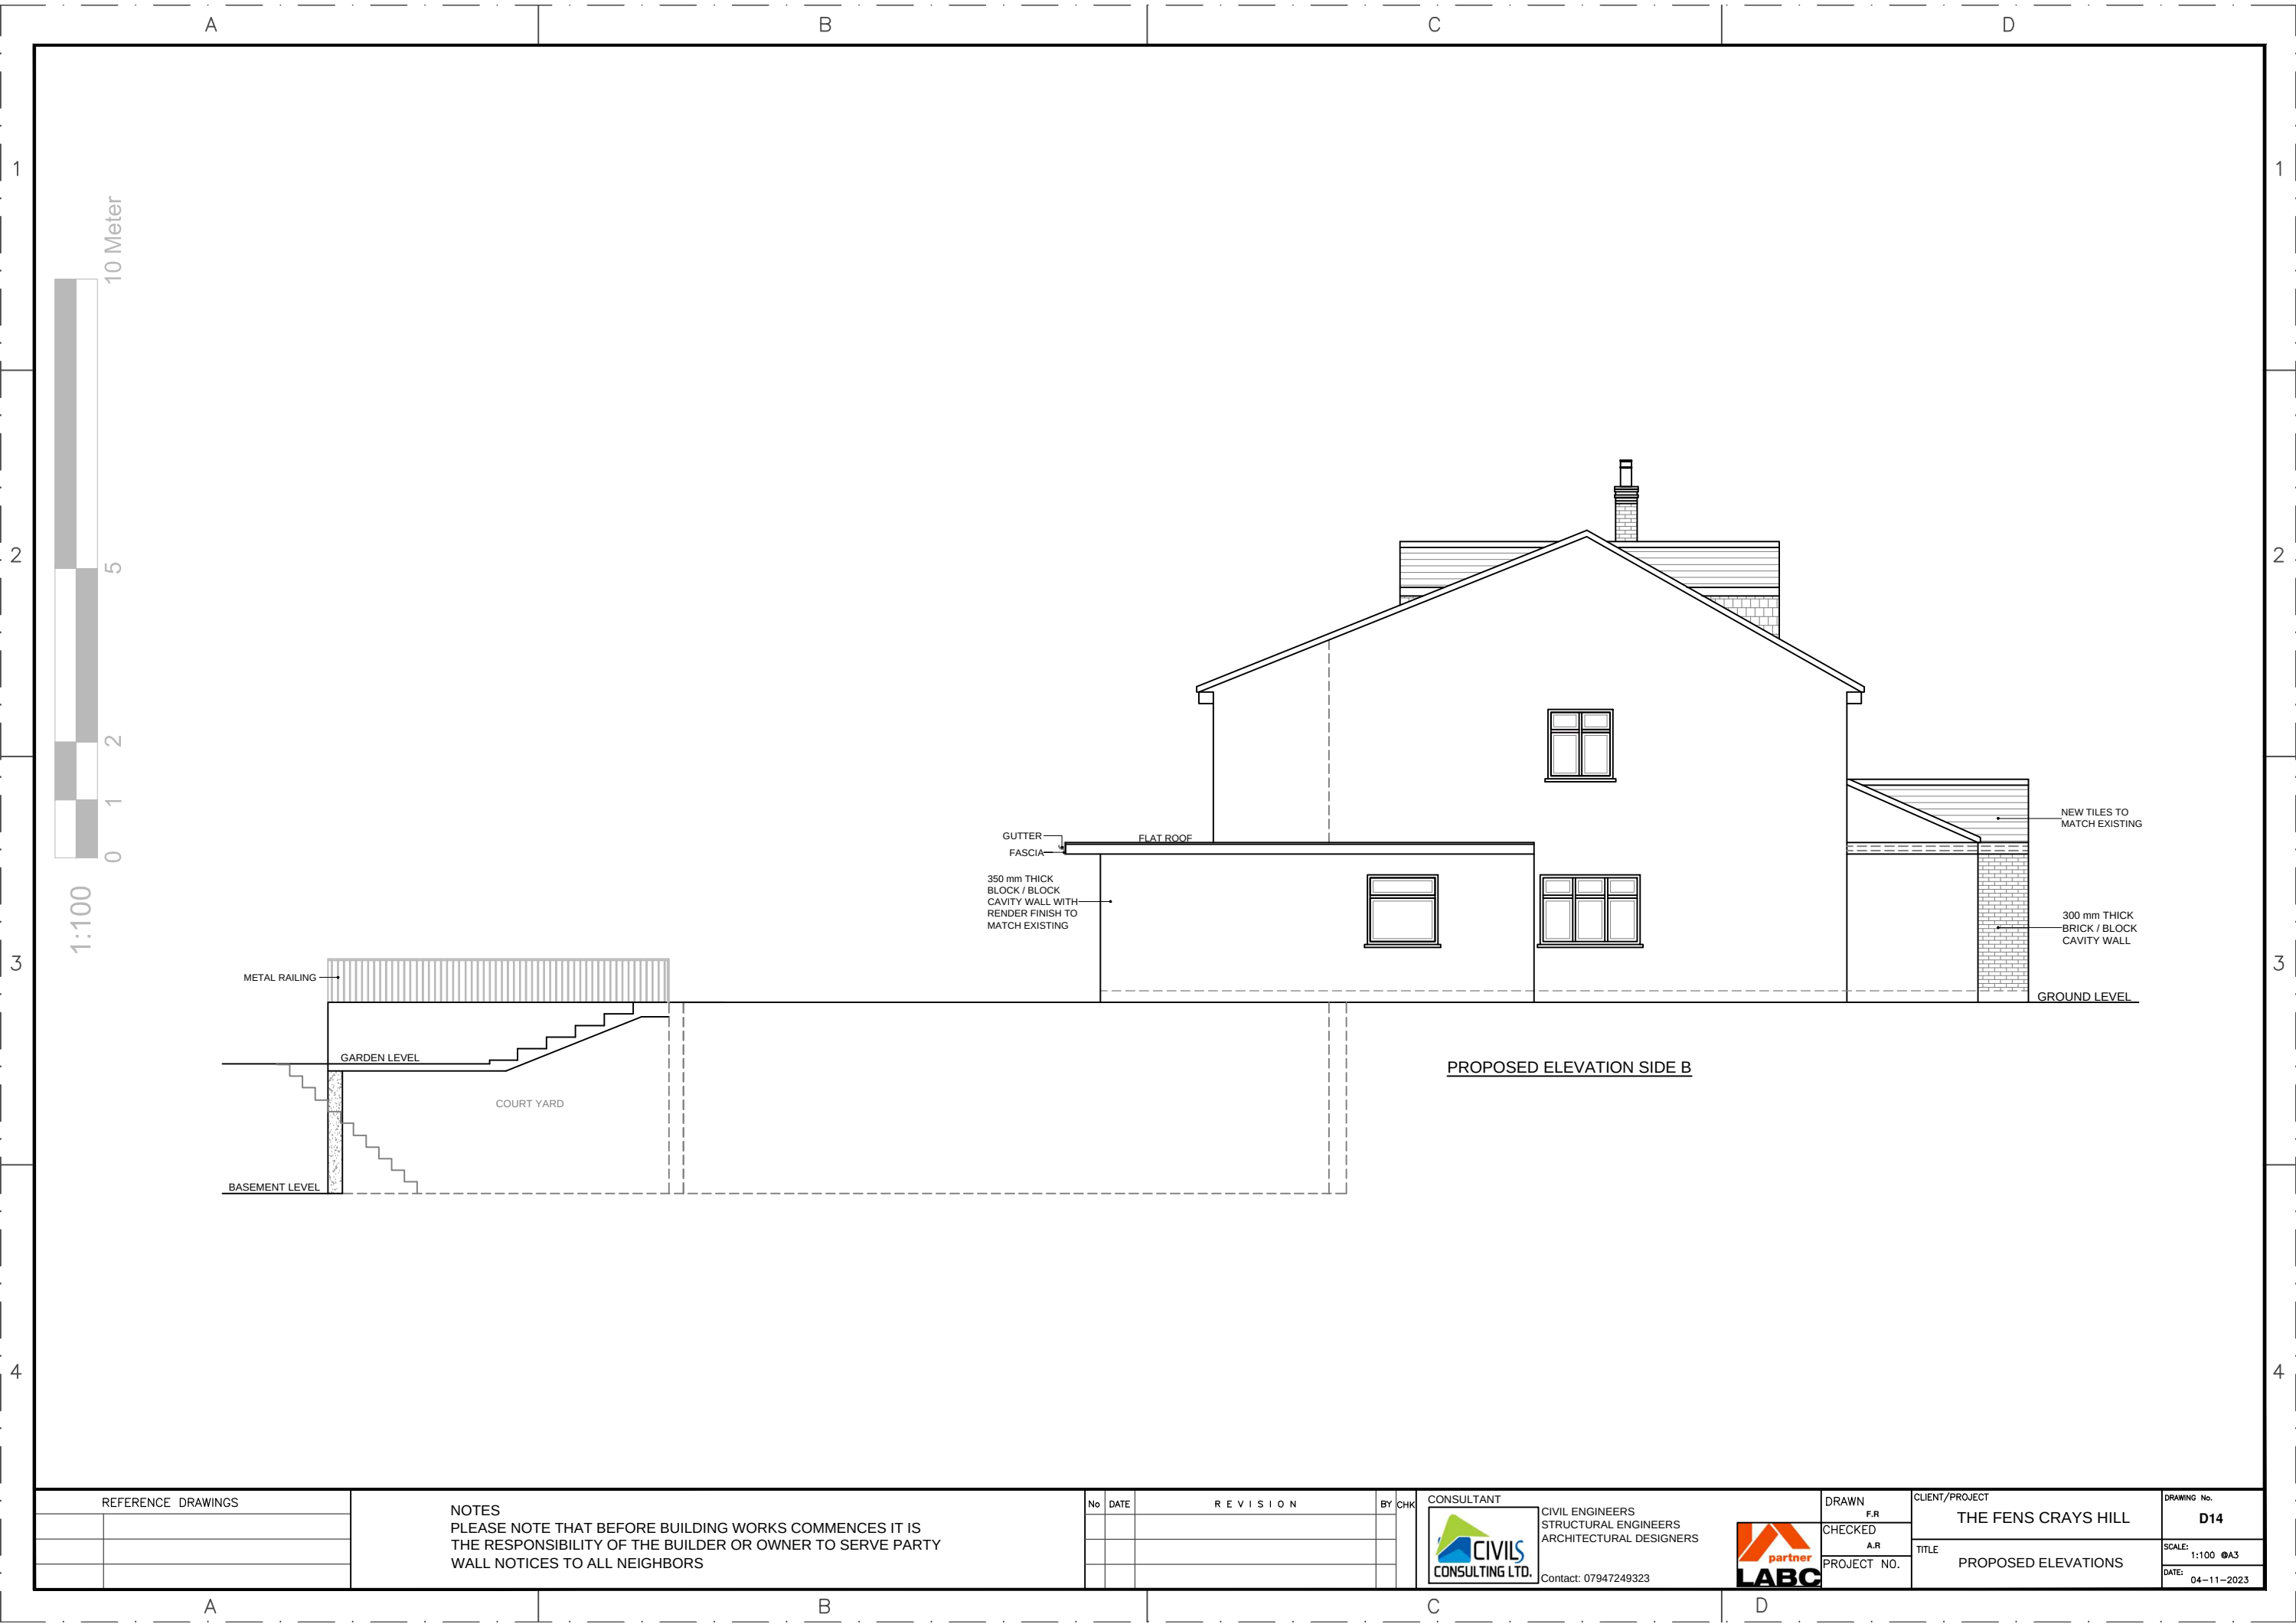

REFERENCE DRAWINGS	

NOTES
PLEASE NOTE THAT BEFORE BUILDING WORKS COMMENCES IT IS
THE RESPONSIBILITY OF THE BUILDER OR OWNER TO SERVE PARTY
WALL NOTICES TO ALL NEIGHBORS

No	DATE	REVISION	BY	CHK

CONSULTANT



CIVIL ENGINEERS
STRUCTURAL ENGINEERS
ARCHITECTURAL DESIGNERS
Contact: 07947249323



DRAWN F.R	CLIENT/PROJECT THE FENS CRAYS HILL	DRAWING No. D14
CHECKED A.R		
PROJECT NO.	TITLE PROPOSED ELEVATIONS	SCALE: 1:100 @A3 DATE: 04-11-2023

GENERAL NOTES


DO NOT SCALE. Work to figured dimensions only. All dimensions, setting out and levels are to be verified on site with the architect prior to the commencement of any site work.

All dimensions are to be verified on site prior to the commencement of any site works. Any variations are to be recorded and reported to the engineer so that the adjustments may be made to the structural scheme if necessary.

The contractor shall be responsible for and must take all necessary precautions to ensure the stability of the existing structure and earthworks on adjoining sites during the course of the contract.


Materials and constructions are to be in accordance with the relevant British Standards and Codes of Practice.

Any services or drainage which pass through the foundation are to be encased in a flexible sleeve.

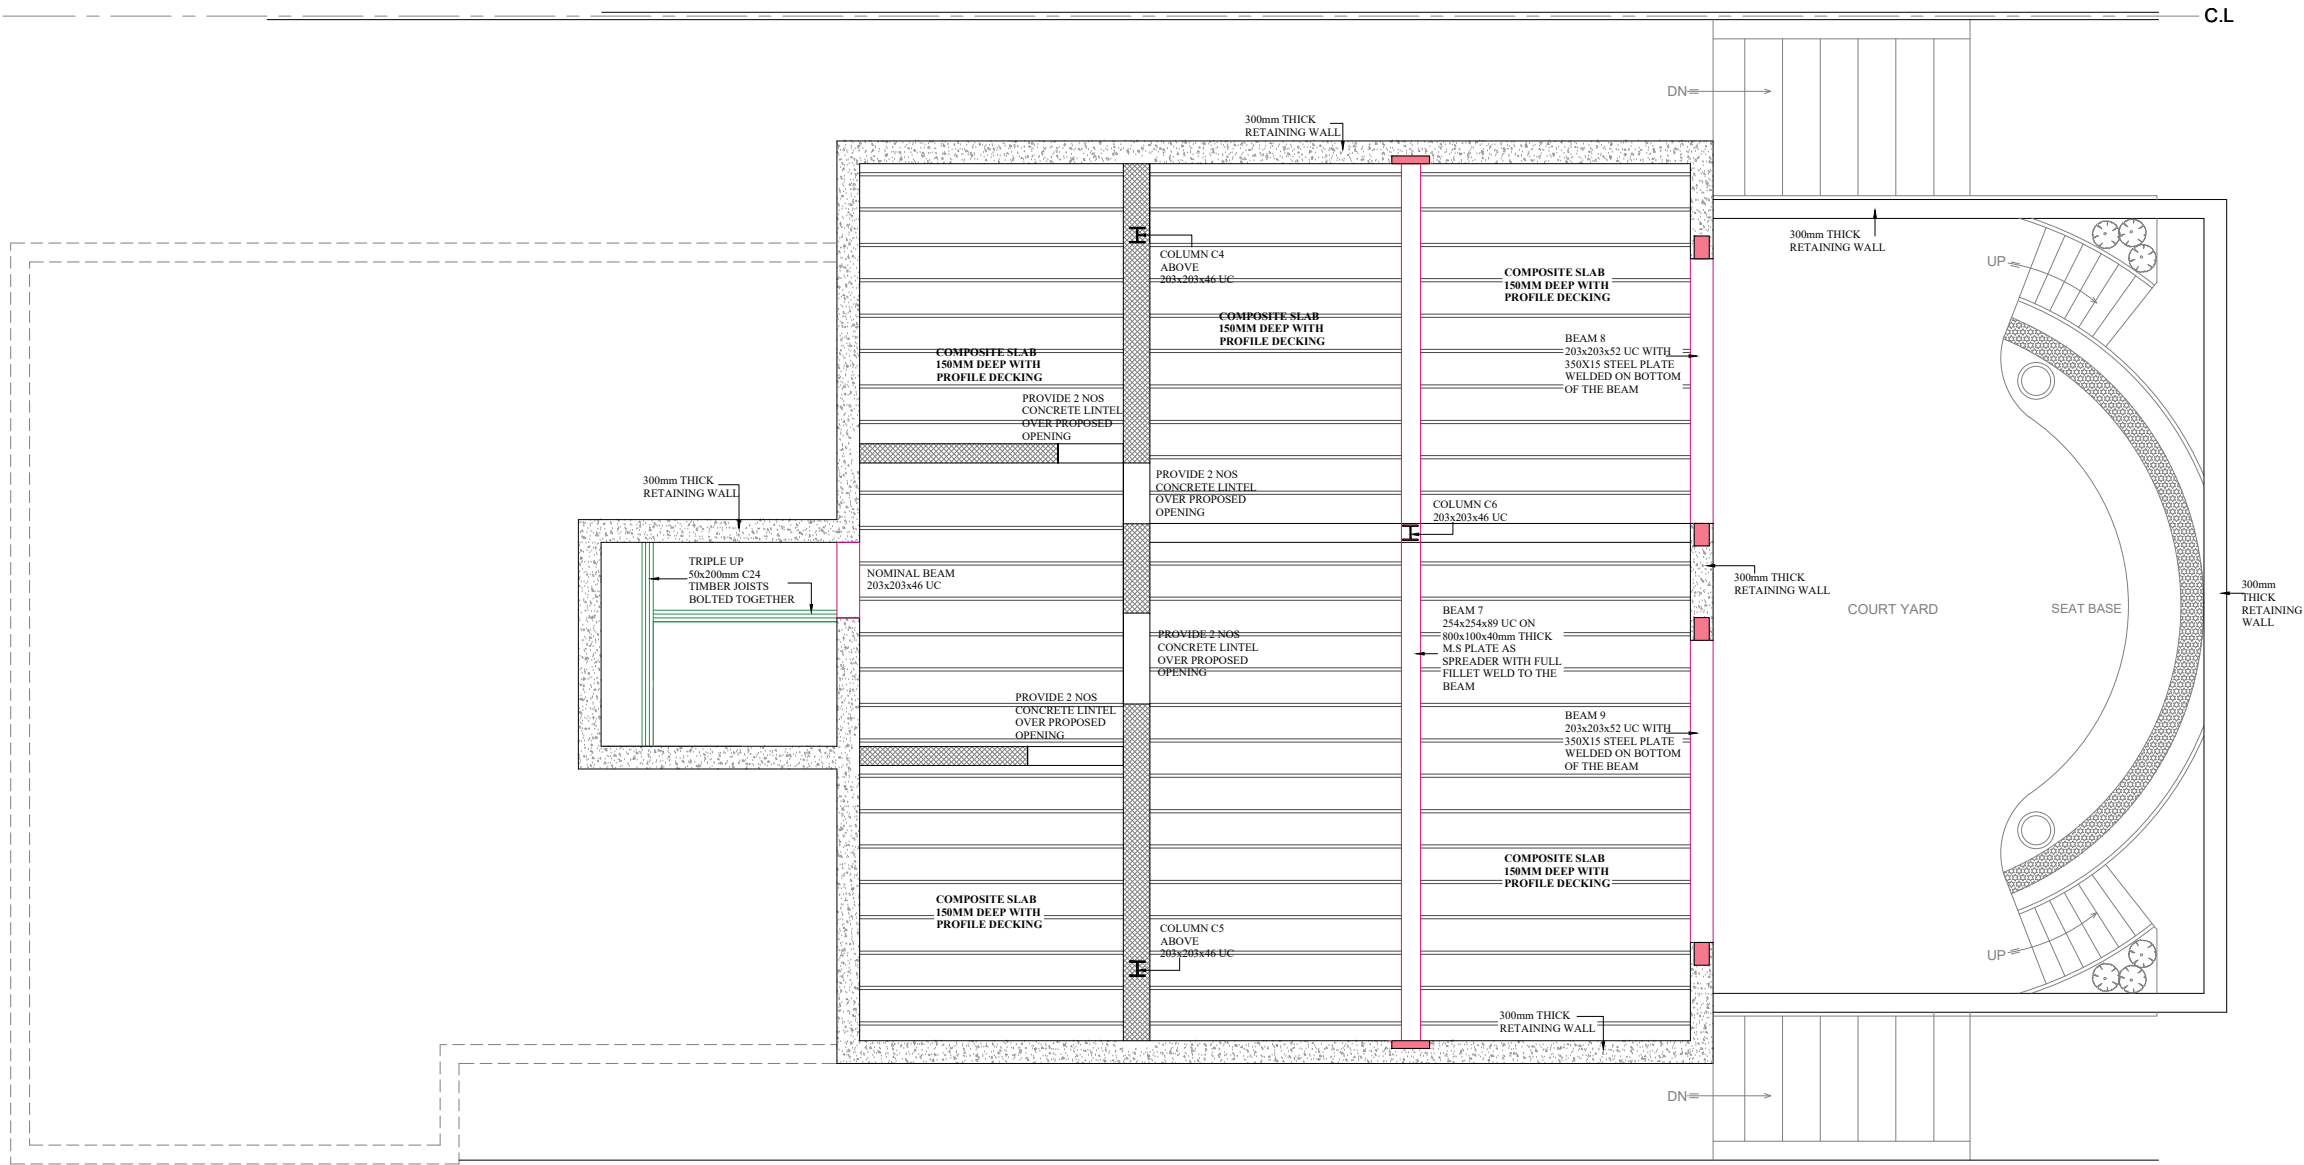

BASEMENT STRUCTURAL LAYOUT

1:100

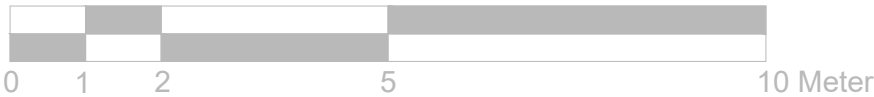

REFERENCE DRAWINGS	

NOTES
PLEASE NOTE THAT BEFORE BUILDING WORKS COMMENCES IT IS THE RESPONSIBILITY OF THE BUILDER OR OWNER TO SERVE PARTY WALL NOTICES TO ALL NEIGHBORS

No	DATE	REVISION	BY	CHK

CONSULTANT
CIVILS
CONSULTING LTD.
Contact: 07947249323
CIVIL ENGINEERS
STRUCTURAL ENGINEERS
ARCHITECTURAL DESIGNERS



DRAWN	F.R
CHECKED	A.R
PROJECT NO.	

CLIENT/PROJECT	THE FENS CRAYS HILL
TITLE	BASEMENT STRUCTURAL LAYOUT

DRAWING No.	D15
SCALE:	1:100 @A3
DATE:	04-11-2023

A

B

C

D

GENERAL NOTES


DO NOT SCALE. Work to figured dimensions only. All dimensions, setting out and levels are to be verified on site with the architect prior to the commencement of any site work.

All dimensions are to be verified on site prior to the commencement of any site works. Any variations are to be recorded and reported to the engineer so that the adjustments may be made to the structural scheme if necessary.

C.L The contractor shall be responsible for and must take all necessary precautions to ensure the stability of the existing structure and earthworks on adjoining sites during the course of the contract.


Materials and constructions are to be in accordance with the relevant British Standards and Codes of Practice.

Any services or drainage which pass through the foundation are to be encased in a flexible sleeve.

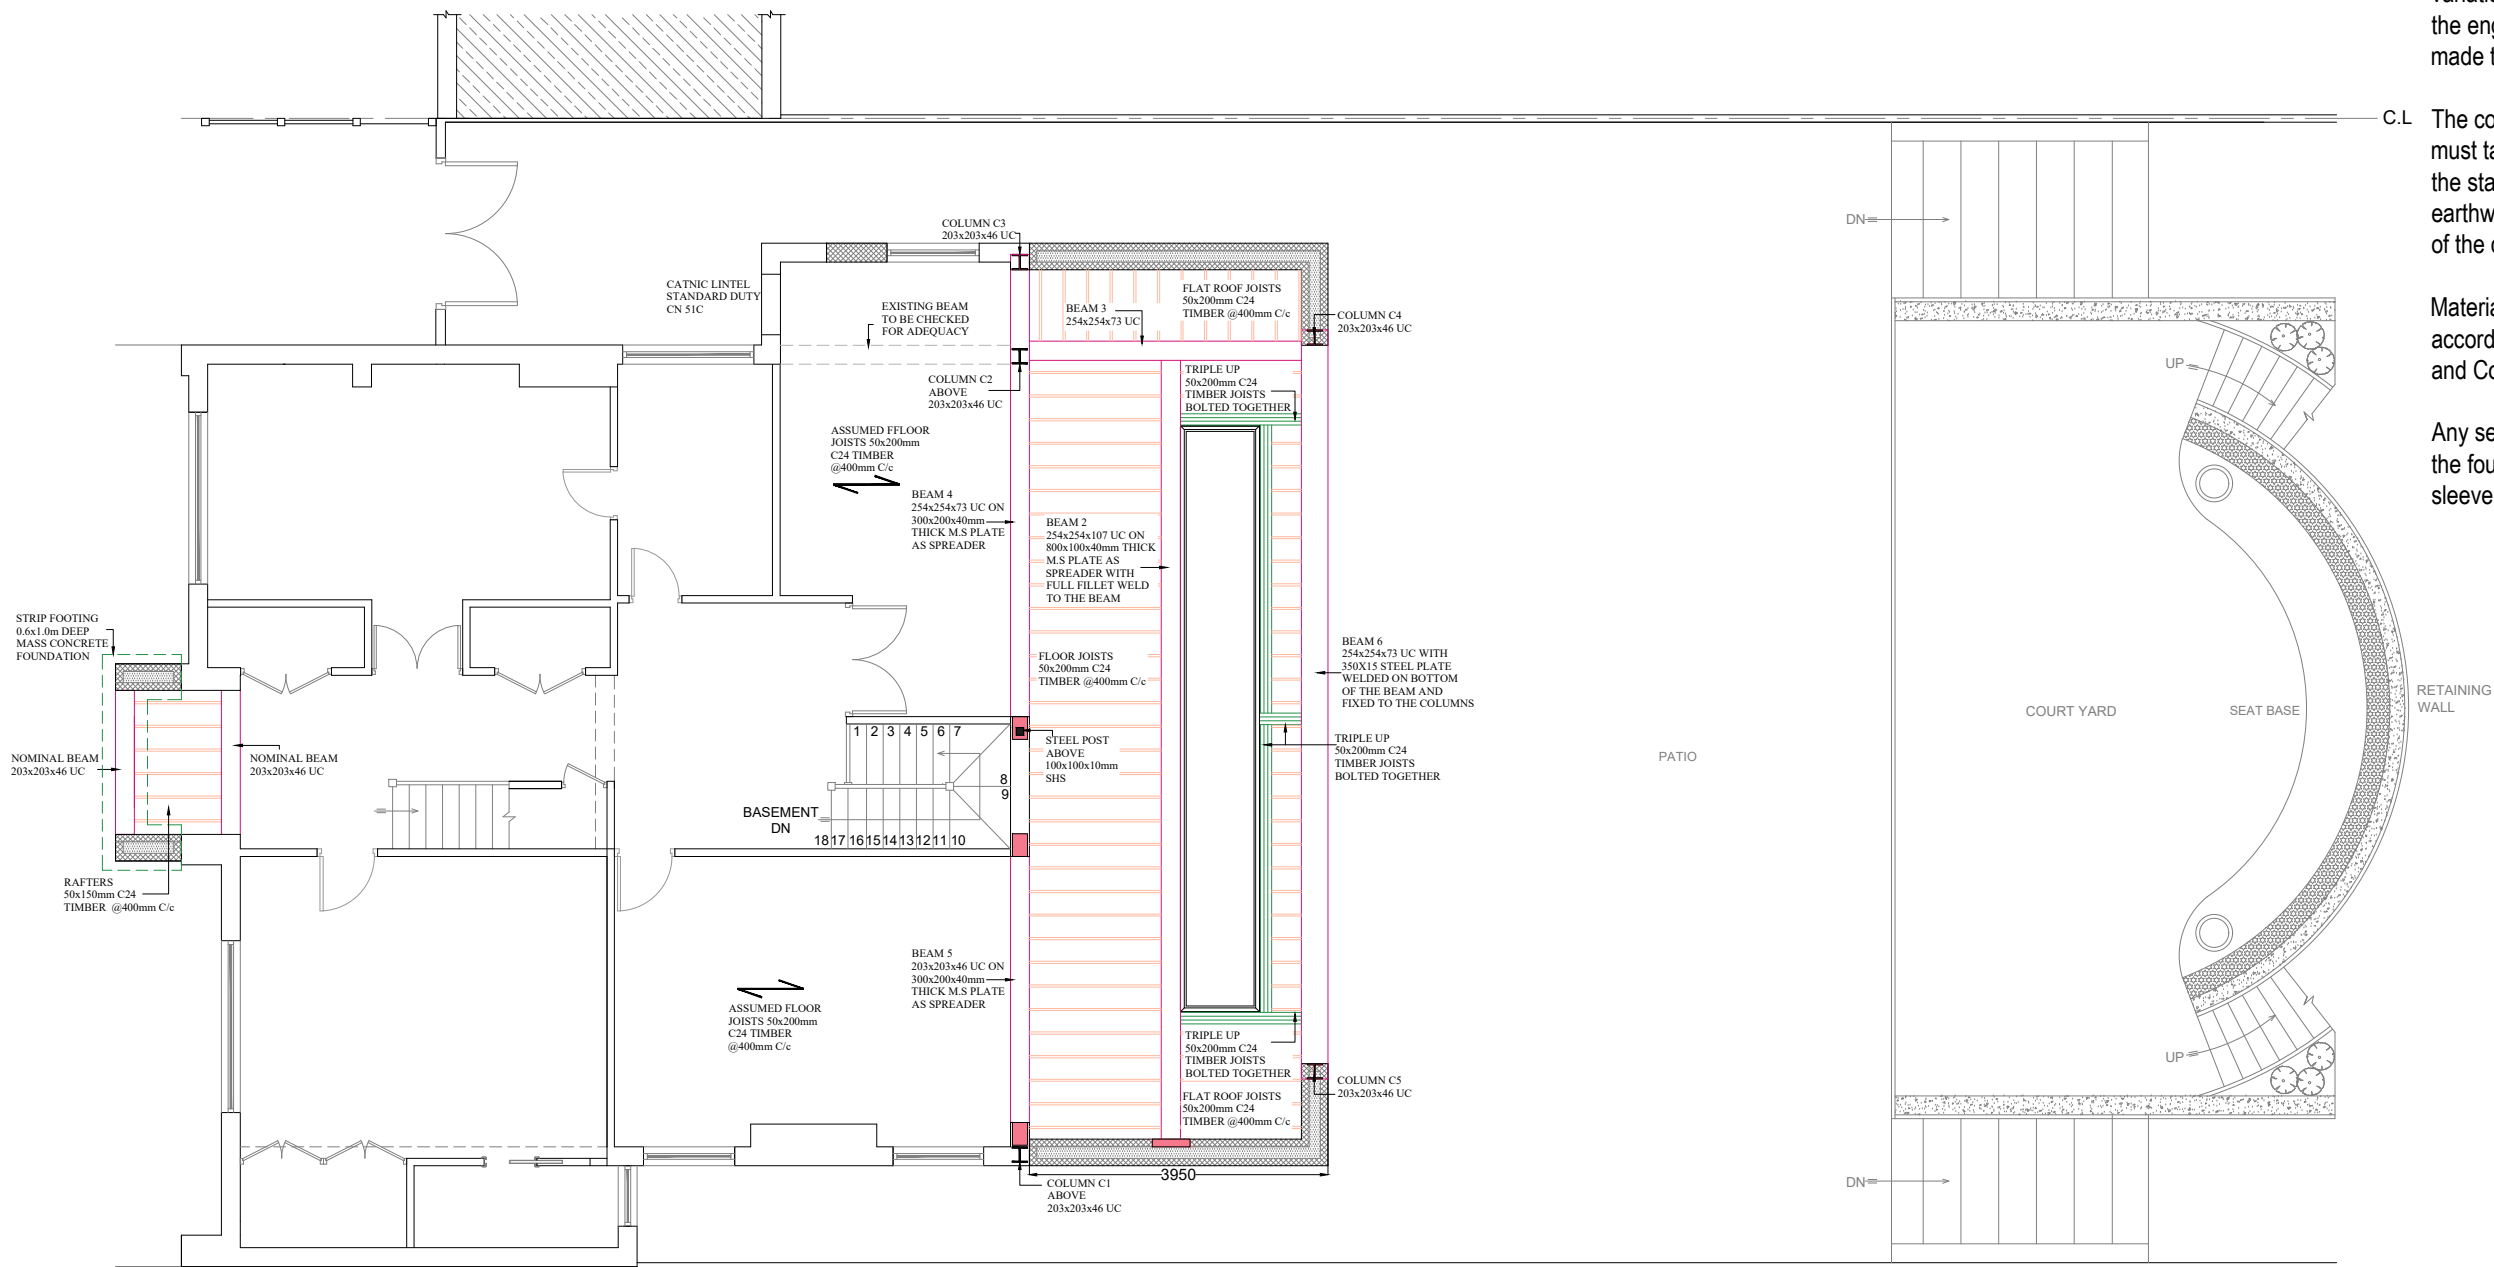

GROUND FLOOR STRUCTURAL LAYOUT

1:100

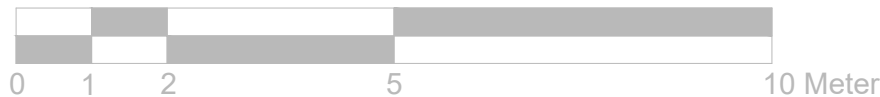

REFERENCE DRAWINGS

NOTES

PLEASE NOTE THAT BEFORE BUILDING WORKS COMMENCES IT IS THE RESPONSIBILITY OF THE BUILDER OR OWNER TO SERVE PARTY WALL NOTICES TO ALL NEIGHBORS

No

DATE

REVISION

BY CHK

CONSULTANT



CIVIL ENGINEERS
STRUCTURAL ENGINEERS
ARCHITECTURAL DESIGNERS
Contact: 07947249323



DRAWN F.R

CHECKED A.R

PROJECT NO.

CLIENT/PROJECT

THE FENS CRAYS HILL

TITLE


GROUND FLOOR
STRUCTURAL LAYOUT

DRAWING No.

D16

SCALE: 1:100 @A3

DATE: 04-11-2023

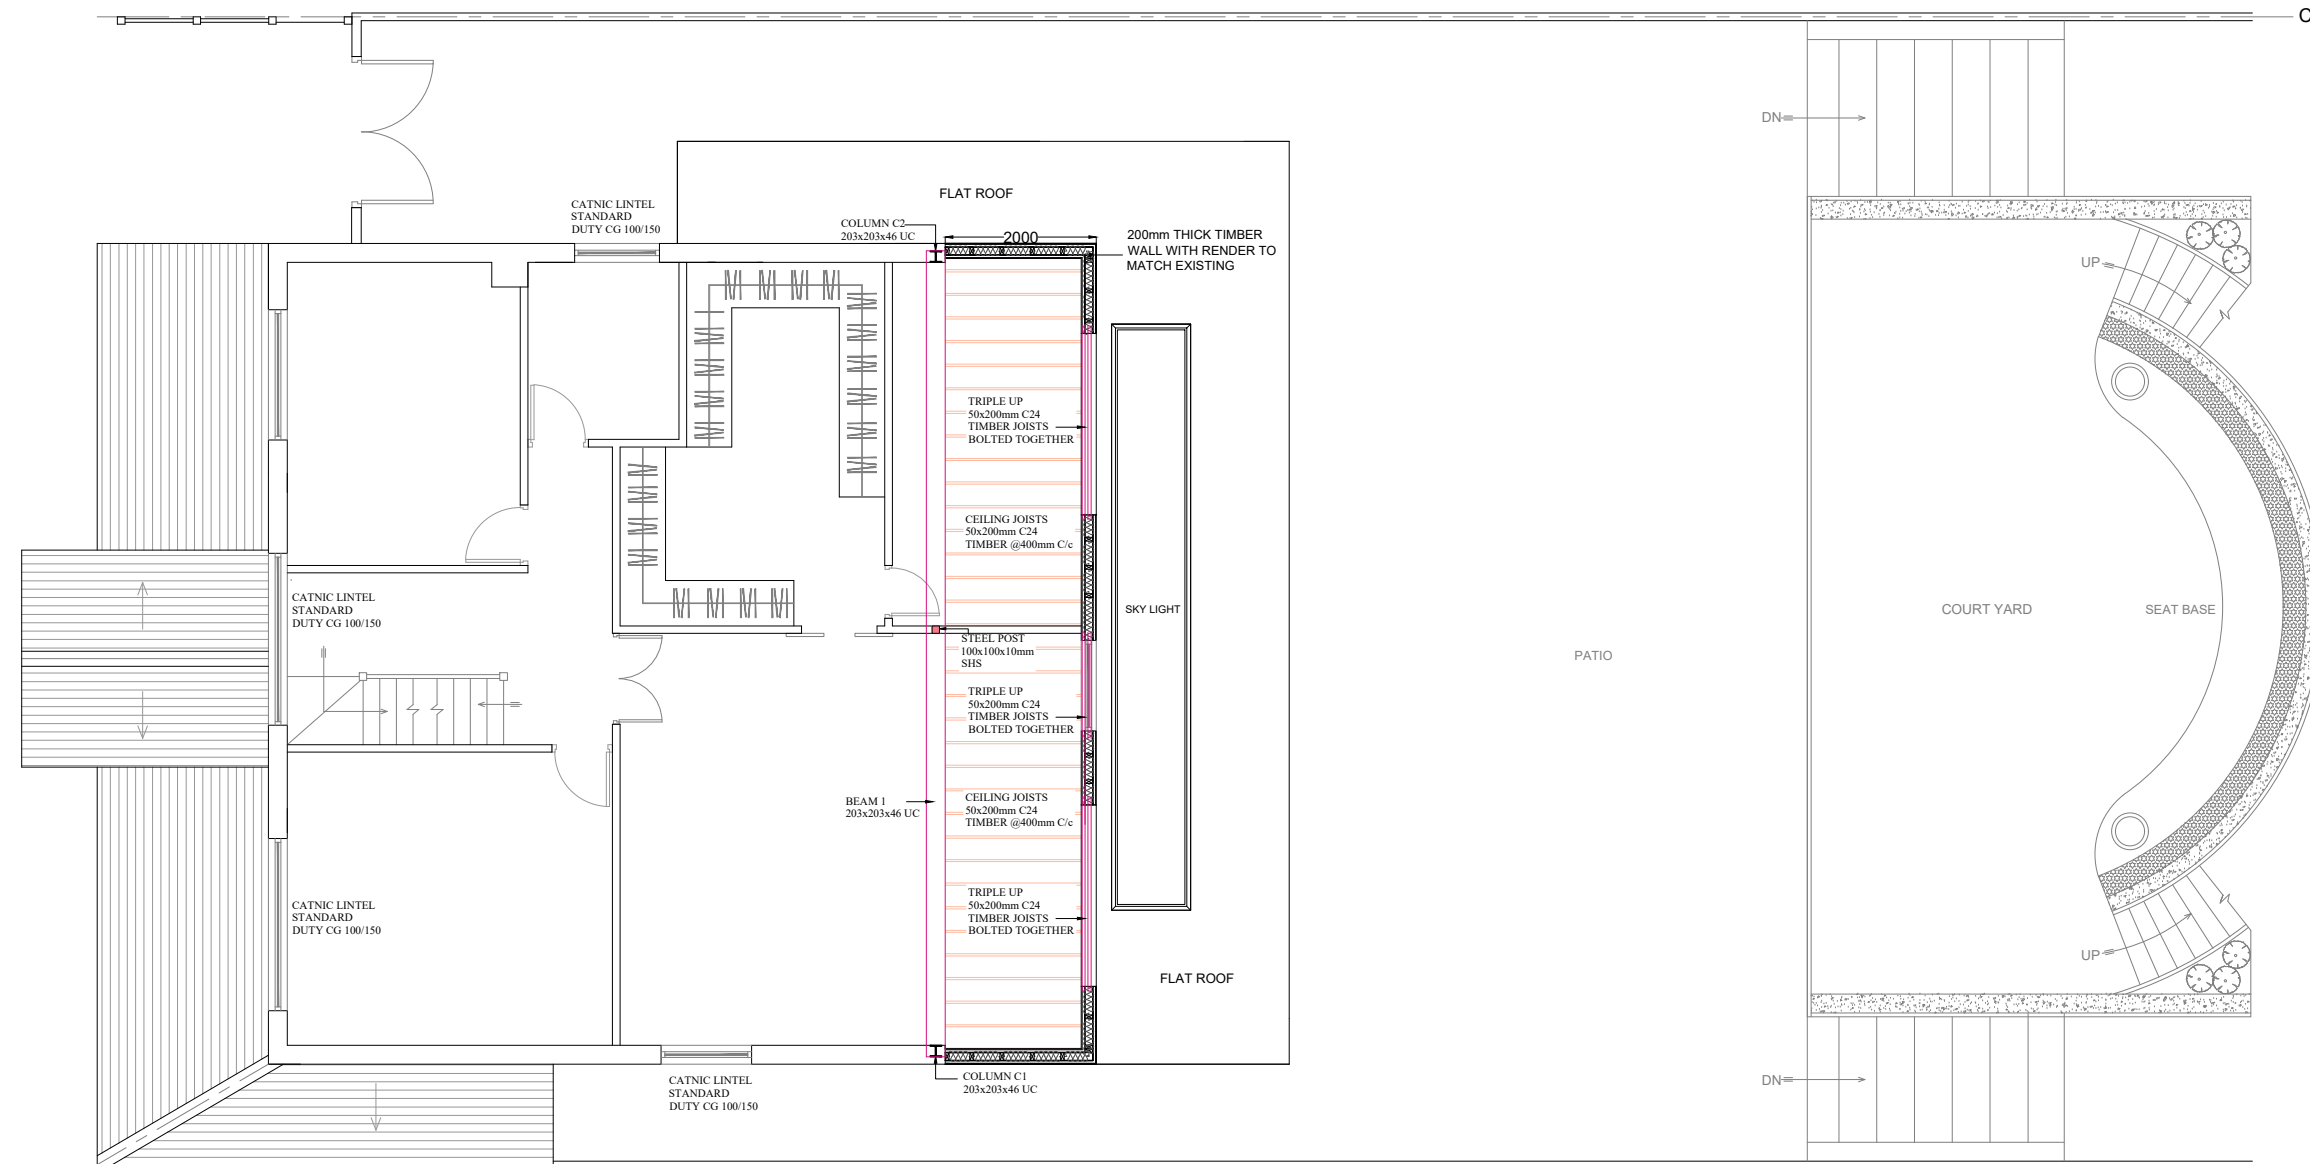

FIRST FLOOR STRUCTURAL LAYOUT

GENERAL NOTES

DO NOT SCALE. Work to figured dimensions only. All dimensions, setting out and levels are to be verified on site with the architect prior to the commencement of any site work.


All dimensions are to be verified on site prior to the commencement of any site works. Any variations are to be recorded and reported to the engineer so that the adjustments may be made to the structural scheme if necessary.

The contractor shall be responsible for and must take all necessary precautions to ensure the stability of the existing structure and earthworks on adjoining sites during the course of the contract.

Materials and constructions are to be in accordance with the relevant British Standards and Codes of Practice.

Any services or drainage which pass through the foundation are to be encased in a flexible sleeve.

1:100

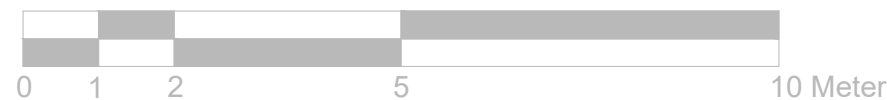

REFERENCE DRAWINGS

NOTES

PLEASE NOTE THAT BEFORE BUILDING WORKS COMMENCES IT IS THE RESPONSIBILITY OF THE BUILDER OR OWNER TO SERVE PARTY WALL NOTICES TO ALL NEIGHBORS

No DATE

REVISION

BY CHK

CONSULTANT



CIVIL ENGINEERS
STRUCTURAL ENGINEERS
ARCHITECTURAL DESIGNERS
Contact: 07947249323



DRAWN F.R

CHECKED A.R

PROJECT NO.

CLIENT/PROJECT

THE FENS CRAYS HILL

TITLE


FIRST FLOOR
STRUCTURAL LAYOUT

DRAWING No.

D17

SCALE: 1:100 @A3

DATE: 04-11-2023

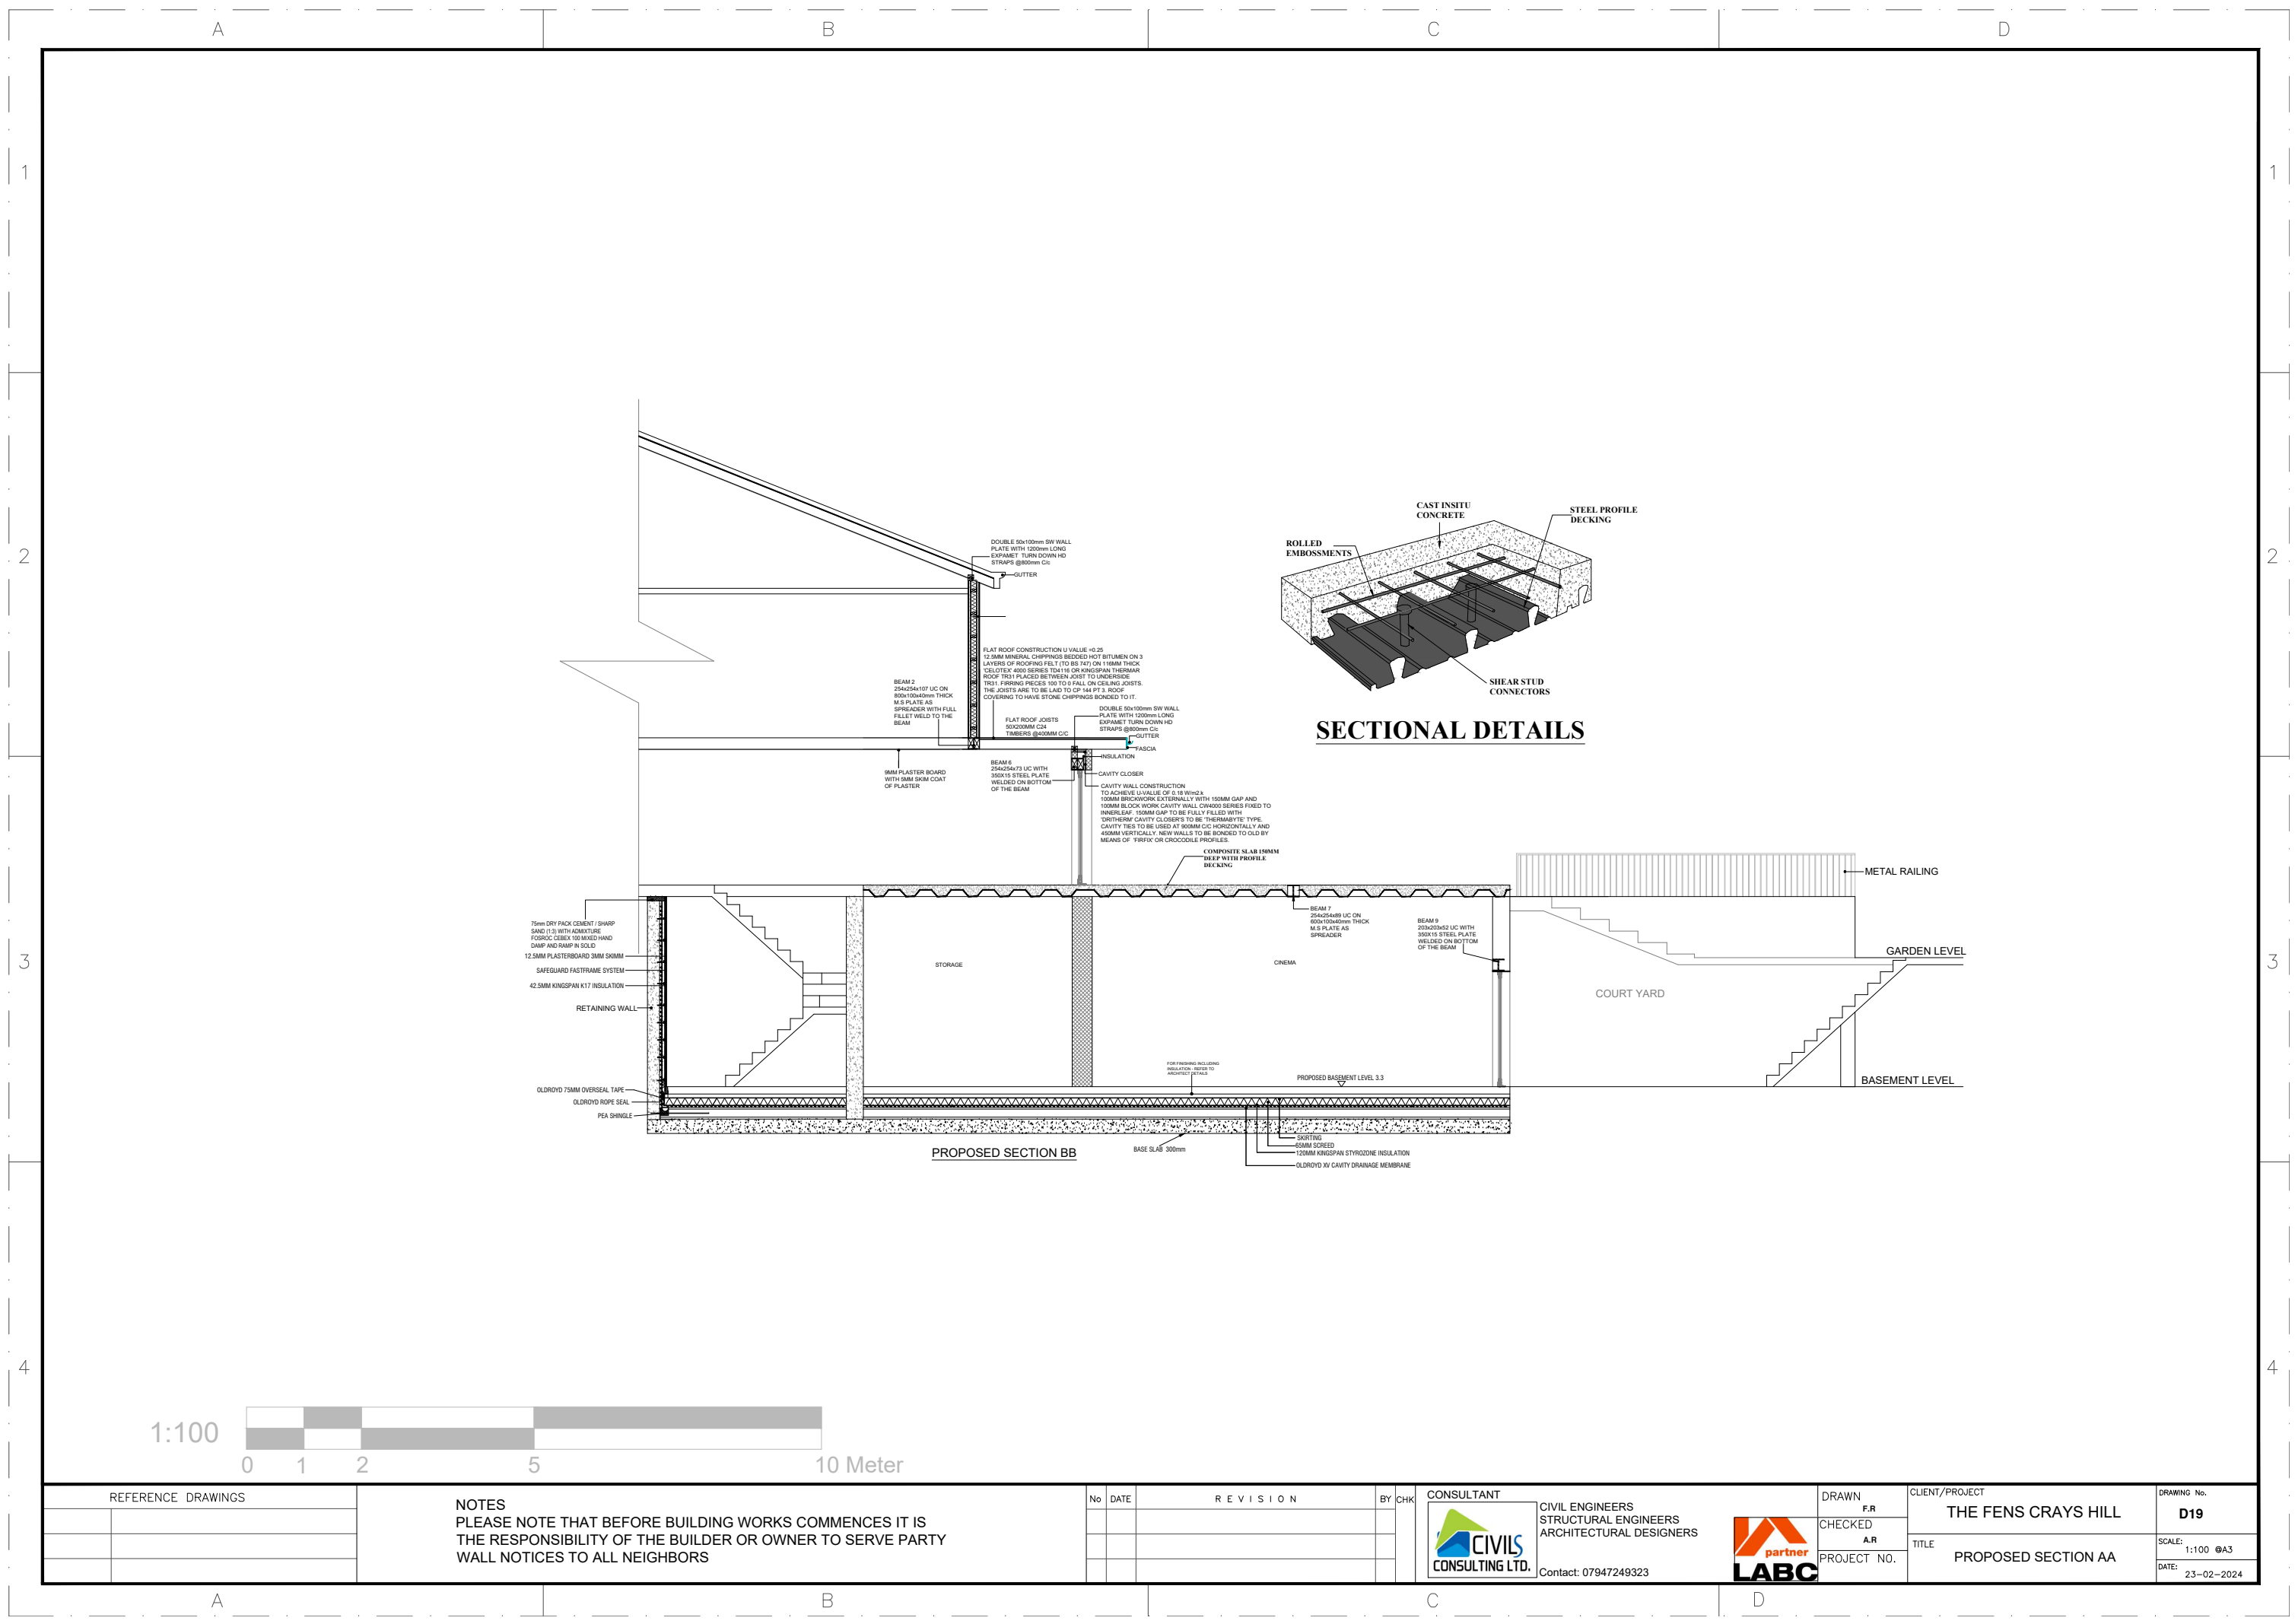



BLOCK PLAN
SCALE: 1:500

REFERENCE DRAWINGS	

NOTES
PLEASE NOTE THAT BEFORE BUILDING WORKS COMMENCES IT IS
THE RESPONSIBILITY OF THE BUILDER OR OWNER TO SERVE PARTY
WALL NOTICES TO ALL NEIGHBORS

No	DATE	REVISION	BY	CHK

CONSULTANT



CIVIL ENGINEERS
STRUCTURAL ENGINEERS
ARCHITECTURAL DESIGNERS
Contact: 07947249323



DRAWN F.R
CHECKED A.R
PROJECT NO.

CLIENT/PROJECT	THE FENS CRAYS HILL
TITLE	BLOCK PLAN

DRAWING No.	D20
SCALE:	1:500 @A3
DATE:	14-02-2024

A

B

C

D

1

2

3


4

1

2



3

4

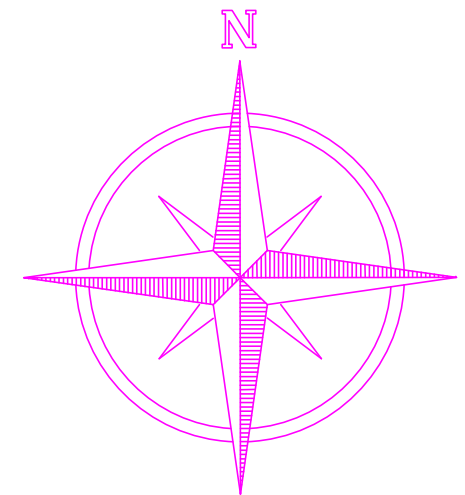

LOCATION PLAN

SCALE: 1:1250

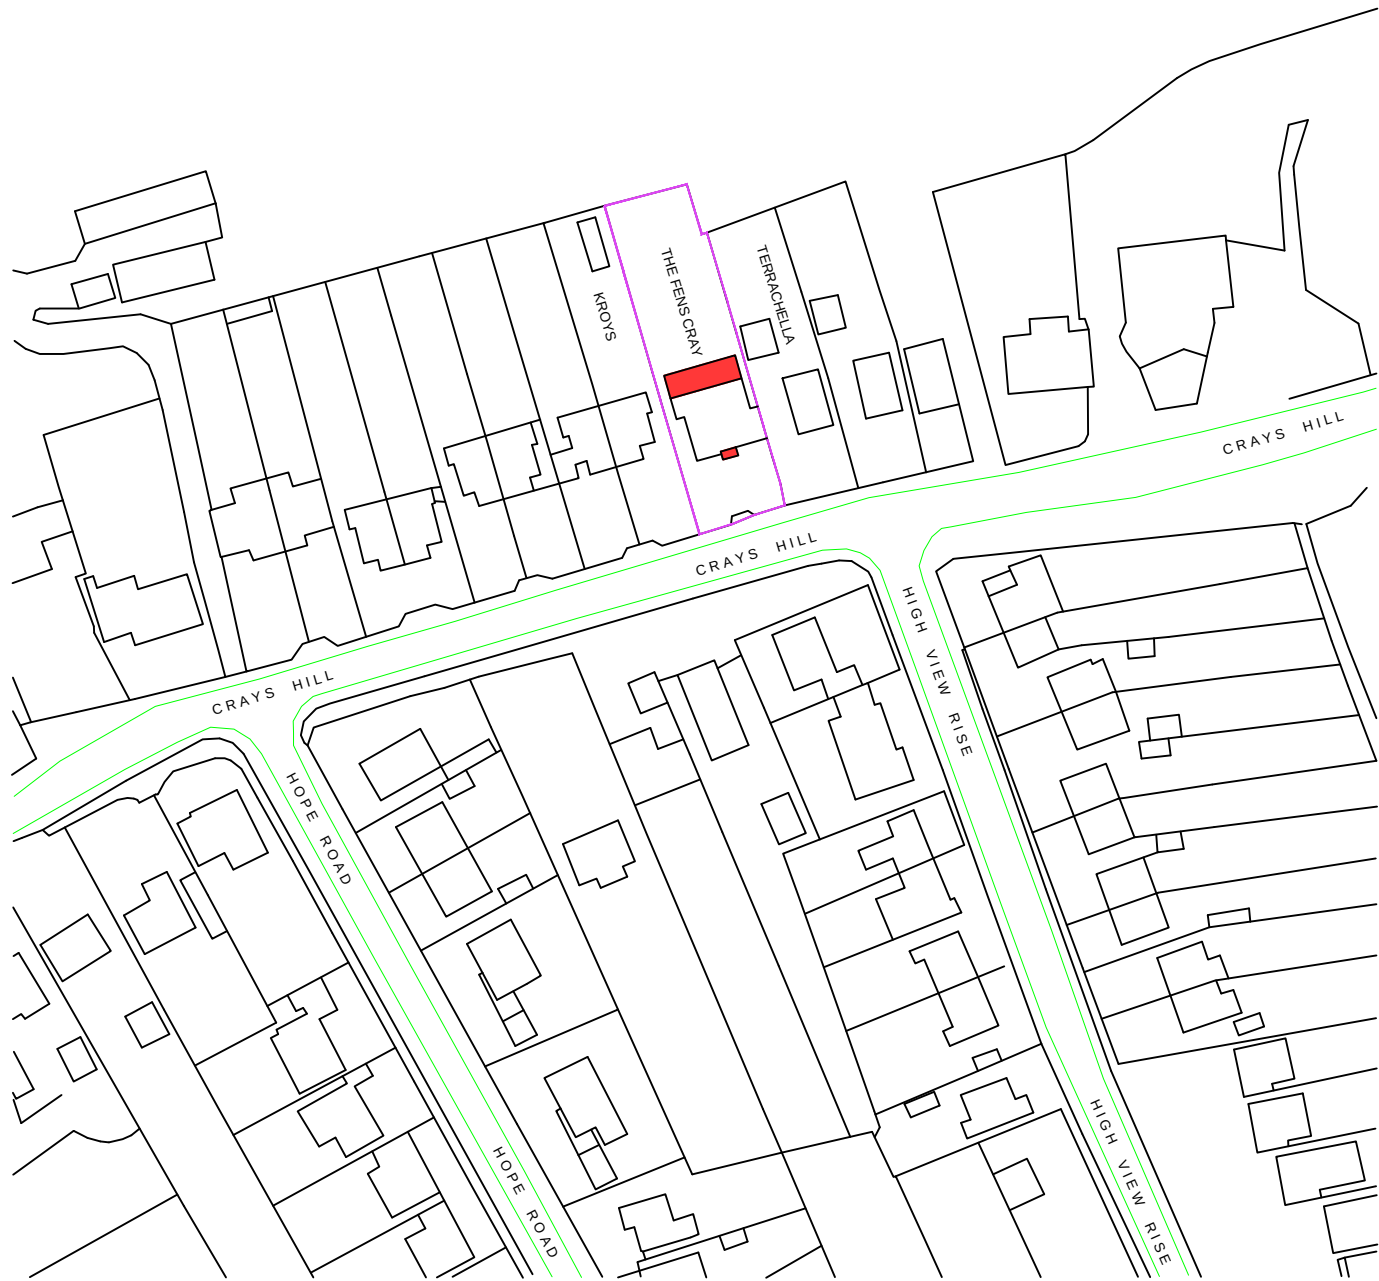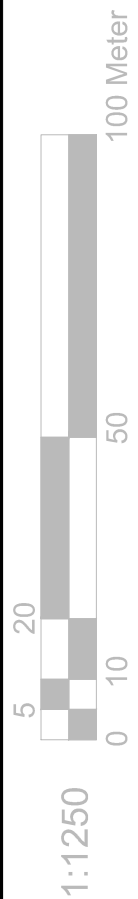

REFERENCE DRAWINGS	

NOTES
PLEASE NOTE THAT BEFORE BUILDING WORKS COMMENCES IT IS
THE RESPONSIBILITY OF THE BUILDER OR OWNER TO SERVE PARTY
WALL NOTICES TO ALL NEIGHBORS

No	DATE	REVISION	BY	CHK

CONSULTANT

**CIVILS**
CONSULTING LTD.

CIVIL ENGINEERS
STRUCTURAL ENGINEERS
ARCHITECTURAL DESIGNERS

Contact: 07947249323



DRAWN F.R
CHECKED A.R
PROJECT NO.

CLIENT/PROJECT
THE FENS CRAYS HILL
TITLE
SITE LOCATION

DRAWING No.
D21
SCALE: 1:1250 @A3
DATE: 14-02-2024

A		B		C		D						
<u>SPECIFICATION</u> All dimensions to be checked on site prior to commencement of works. Any discrepancies to be notified to the designer . Client to ensure all of contractors' works on site to comply with and meet Approval of the relevant British Standards and the Local Authority including Building Control and Planning Departments. <u>Party Wall Notices</u> should they be required, and their serving are wholly the responsibility of the owner/occupant of the site and should be served prior to commencement of any works. <u>Public Sewers</u> The design has been made assuming there is no 'Public Sewer' present in the vicinity. It is the owner/occupant's responsibility to confirm that this is the case. (ie This may require the owner/occupant to confirm that a Build Over Agreement has been entered into with the Water Utilities Company) <u>Windows</u> to be double glazed and to be to BS 6206 fitted with safety glass. Double Glazing to 16mm air gap with 'Soft' Low E-Coating Open able windows to be 1/20th of the floor area. Areas of doors and windows not to exceed 25% floor area. Natural light to be 1/10th of floor area. <u>Foundations</u> to be 1m deep x 0.6m wide trench footings with mass concrete 1:2:4 Mix. (Depth of footings to be in accordance with NHBC practice ie minimum of 1m depth or the depth of the invert level of drains in proximity if deeper. Soil conditions to be verified on site by Local Authority Building Control Department on site prior to commencement. Foundations may be eccentrically loaded along boundary. All existing foundations and lintels to be exposed to verify suitability and to be checked for adequacy and/or replaced or surrounded in 150mm concrete cover if necessary. Prior to commencement a trial hole and /or soil report/investigation and an inspection of any trees in the areas may be required to confirm traditional 'trench footing' scheme is acceptable to Local Authority. <u>Soil & Waste Drainage</u> to be in accordance with CP 8201 and materials to be in line with BS 5572. New wastes to be in PVC. Deep seal traps to be a minimum of 75mm to all sanitary ware. Wash Hand Basins 32mm dia Sink Wastes 38mm dia Shower Wastes 43mmmm dia Wastes to W.C. 100mm dia Rainwater 63mm dia Underground drains to be in PVC 100mm dia bedded in pea shingle 150mm all round with a minimum fall of 1:40 Any drains passing through the footings to be protected by reinforced concrete lintels <u>Surface Water</u> to discharge to separate surface water drains or soak away minimum of 6m from foundations to BRE recommendations. <u>Foul water</u> to discharge to on site foul water system. Any redundant drains or Back Inlet Gullys to be grubbed up. <u>Cavity Wall Construction</u> to have a U-Value of 0.18 100mm brickwork externally with 150mm gap and 100mm block work cavity wall cw4000 series fixed to inner leaf. 150mm gap to be fully filled with 'dritherm' cavity closer's to be 'thermabyte' type. cavity ties to be used at 900mm c/c horizontally and 450mm vertically. new walls to be bonded to old by means of 'firfix' or crocodile profiles. CAVITY WALL CONSTRUCTION to achieve u-value of 0.18 w/m2.k 100mm block externally with 150mm gap and 100mm medium weight block cavity wall cw4000 series fixed to innerleaf. 150mm gap to be fully filled with 'dritherm' cavity closer's to be 'thermabyte' type. cavity ties to be used at 900mm c/c horizontally and 450mm vertically. new walls to be bonded to old by means of 'firfix' or crocodile profiles. <u>SOLID BLOCK Wall</u> to have a U-Value of 0.30 265mm wall in thermalite turbo or similar thermal plasterboard 45mm thermal line plus <u>External Walls</u> to be to 265mm thick Celcon Solar Blocks and 35mm thick Gyproc Thermal Board internally. <u>100mm Stud Partitions</u> Made from 100x50 braced studwork, 12.5mm plasterboard and set both sides and with double joists under parallel partitions <u>Internal Returns</u> to existing front, rear or side elevation masonry to be minimum of 550mm wide <u>Emergency Egress</u> to 1st floor or higher windows to be retained via the provision of 450mm x 750mm clear window openings. Cill heights to be between 800mm to 1100mm. Mains connected smoke detector at the top and bottom of stairs. <u>Concrete Floor</u> to have a U-Value of 0.25. 65mm Sand and Cement Screed 1:4 Mix 100mm Plain concrete DPM Gauge 1200 to overlap minimum of 150mm vertical DPC 125mm Polystyrene (Jablite) on sand blinding on minimum of 150mm mechanically compacted hardcore base. Any existing air vents to be maintained to external air via sub floor vents maximum of 1.35m spacing with minimum of 3 Nos. 75mm dia ducts. <u>DPC</u> to be minimum of 150mm above ground floor level to BS 743 Vertical and Horizontal DPC to all reveals to be mastic or cellular plastic Expansion joints to walls be provided @ 6m c/c vertically & minimum of 3m from any corner. Joint to be 'Corkpak' type. <u>Guttering</u> to be 100mm PVC ½ round guttering on 20mm fascia board <u>Position and Depth of Manhole/s</u> to be confirmed before any excavations carried out. Any New manhole to comprise of 225mm semi engineering bricks on 150mm solid concrete slab (and double seal ed to BS 497, if internal). <u>Warm Deck Flat Roof Construction</u> U Value =0.15 w/m2.k 12.5mm mineral chippings bedded hot bitumen on 3 layers of roofing felt (to bs 747) on 165mm thick 'celotex' xr4000 series or kingspan thermar roof tr31 placed between joist to underside tr31. furring pieces 100 to 0 fall on ceiling joists. the joists are to be laid to cp 144 pt 3. roof covering to have stone chippings bonded to it. <u>Dormer Stud Work</u> to have a U-Value of 0.30 125x50 Timber frame at 400 centres with tile hanging to outside face with Celotex 3000 series 112mm thick between studs <u>Pitched Roof Tiles</u> to be 418x332 Redland Regent (or similar approved) on felt & battens with 75mm overlap. <u>Pitch Roof</u> Insulation between ceiling joists at 400 centres Insulation fibreglass 100mm between and 200mm across <u>Sloping ceiling</u> In new building or extension rafters at 400 centres 50mm airspace over with celotex 3000 series 50mm between and 75mm across underside <u>Roof Ventillation</u>: Low level to be achieved via 25mm wide air gap for air flow. High Level ventilation to be achieved via Hi-Level vents @ 2m centres or a raised 'ridge vent' tile. <u>Roof Insulation</u> in Loft space to be 300mm thick Rockwool insulation laid 100mm between timbers and 200mm across, Provide 12.5mm Plasterboard and Skim coat. U-value to be 0.18w/m2K. <u>Code 4 Lead flashing</u> with 150mm vertical upstand to be inserted at the junction of the 'flat' felt roof and the vertical. <u>Trickle Ventillation</u> to any 'Habitable' rooms to be 8000mmsq and Bathroom 4000mmsq. <u>Catnic Lintels</u> to be installed over window openings unless otherwise stated with 150mm end bearing. <u>Mechanical Ventillation</u> to kitchen 60 litres/sec, to bathroom 50 litres/sec <u>Internal Ceiling</u> to have 12.5mm Plasterboard foil backed with 5mm skim coat. <u>Restraint Strapping</u> to Wall Plate/Roof joists to be 30x5mm galavanised holding down straps at 1.5m centres. <u>All Steel Beams</u> to have minimum of 1/2hr Fire Resistance via 'Nullifire' Paint Or 19mm Gyproc Plank tied with 1.6mm wire binding @ 100mm c/c and finished in Carlite Bonding 16mm thick. <u>Lighting</u> Minimum of one new fixed light point should only be capable of taking bulbs with an efficiency exceeding 40 lumens per circuit-watt <u>Electrical</u> Prior to completion the Local Authority should be satisfied that any such work (other than that defined as minor work) complies with Part P. This will require an appropriate BS 7671 Electrical Installation Certificate to be issued by a person authorised to do so (i.e. a person who is registered under a recognised competent persons scheme for self-certification.)												
REFERENCE DRAWINGS		NOTES PLEASE NOTE THAT BEFORE BUILDING WORKS COMMENCES IT IS THE RESPONSIBILITY OF THE BUILDER OR OWNER TO SERVE PARTY WALL NOTICES TO ALL NEIGHBORS	No	DATE	REVISION	BY	CHK	CONSULTANT	DRAWN F.R	CLIENT/PROJECT THE FENS CRAYS HILL	DRAWING No. D22	
									CIVIL CONSULTING LTD.	CHECKED A.R	TITLE SPECIFICATIONS	SCALE: NTS @A3
									Contact: 07947249323	PROJECT NO.		DATE: 04-11-2023

A		B		C		D						
LOFT CONVERSION SPECIFICATIONS												
ALL WORK TO BE CARRIED OUT IN ACCORDANCE WITH BUILDING REGULATIONS AND BRITISH CODES OF PRACTICE.												
DIMENSIONS TO BE CHECKED ON SITE BEFORE WORK COMMENCES AND BUILDER TO REPORT ANY DISCREPANCIES BEFORE WORK COMMENCES. THIS INCLUDES AN ASSESSMENT OF WHETHER THERE WILL BE ANY SIGNIFICANT PROBLEM IN CARRYING OUT THE WORK ON SITE AS PER THE DRAWING.												
THE BUILDER IS ASSUMED TO HAVE A WORKING KNOWLEDGE OF THE BUILDING REGULATIONS AND WORK ON SITE MUST FOLLOW THE LATEST BUILDING REGULATIONS AS AND WHEN THE LOCAL AUTHORITY SURVEYOR REQUIRES.												
ANY LINTOLS OVER WINDOW AND DOOR OPENINGS MAY HAVE TO BE EXPOSED ON SITE IN ORDER TO CONFIRM SUITABILITY TO SUPPORT THE ADDITIONAL LOADS. INADEQUATE LINTOLS WILL REQUIRE RENEWAL AS NECESSARY.												
THE BUILDING OWNER IS RESPONSIBLE FOR SERVING ANY PARTY WALL NOTICES ON NEIGHBOURS PRIOR TO BUILDING WORKS COMMENCING.												
THE BUILDER WILL HAVE TO REFER TO CALCULATION SHEETS FOR STRUCTURAL DETAILS IN ADDITION TO THE DRAWING FOR ITEMS SUCH AS CONNECTIONS.												
1.STAIRCASE												
GOING = 220 MM. RISER= 198 MM. ANGLE OF STAIRS = 42 DEGREES. HEIGHT OF HANDRAIL = 940 MM. HEADROOM OVER STAIRCASE = 2050 MM MINIMUM. MINIMUM GOING AT NEWEL POST = 50 MM. MINIMUM DEPTH OF LANDING AT TOP/BOTTOM OF STAIRS IS 500MM WITH INWARD OPENING DOOR.												
NO GLAZED AREAS TO THE STAIRCASE, OTHERWISE USE WIRED GLASS.												
BALUSTRADE TO STAIRCASE TO HAVE MAXIMUM GAP OF 100MM IN ORDER THAT A SPHERE OF 100MM DIAMETER IS UNABLE TO PASS THROUGH.												
NEWEL POST TO WINDERS TO BE 100MM SQUARE TIMBER SECTION AND TO BE SUPPORTED UPON DOUBLED UP FLOOR JOISTS AT FIRST FLOOR LEVEL.												
2.VENTILATION												
ANY BATHROOM OR W.C. TO THE LOFT AREA TO HAVE MECHANICAL VENTILATION TO EXTRACT AT 15 LITRES PER SECOND WITH 20 MINUTE OVERRUN. THE EXTRACTOR TO DISCHARGE TO EXTERNAL AIR. WINDOWS TO HAVE OPENABLE AREAS TO ALL ROOMS IN ORDER TO PROVIDE NATURAL VENTILATION REQUIREMENT OF 1/20TH FLOOR AREA. HABITABLE ROOMS TO HAVE BACKGROUND OR TRICKLE VENTILATION EQUIVALENT TO 8,000 SQ.MM. EAVES VENTILATION SHOULD BE PROVIDED OR MAINTAINED WITH MINIMUM 25MM WIDE AIR GAP WITH FLY MESH COVER. WHERE EAVES ARE NOT VENTILATED OR OVERHANGING, THEN PROVIDE LOW LEVEL VENT TILES AT 1.3M CENTRES TO SLOPING ROOF AND SIMILAR AT HIGH LEVEL IN ORDER TO MAINTAIN THE THROUGH VENTILATION.												
3.GLAZING												
NEW GLAZING TO BE DOUBLE GLAZING WITH 16MM AIR GAP AND LOW E- COATING (K- GLASS). GLAZED AREAS TO BE 1/10TH FLOOR AREA IN ORDER TO PROVIDE FOR NATURAL LIGHT REQUIREMENTS.												
4.WASTES												
BATH WASTE TO BE 43MM DIAMETER PVC BASIN WASTE TO BE 37MM DIAMETER PVC W.C. WASTE TO BE 100MM DIAMETER PVC SHOWER WASTE TO BE 50MM DIAMETER PVC TRAPS TO BE 75MM DIAMETER DEEP SEAL. ACCESS AND RODDING POINTS TO ALL CHANGES IN DIRECTION. GUTTER TO DORMER ROOF TO BE 100MM HALF ROUND PVC, AND RAINWATER DOWNPIPE DISCHARGING ONTO REAR SLOPING ROOF OR RUNNING DOWN TO THE RAINWATER GULLEY IS 63MM DIAMETER PVC. AIR ADMITTANCE VALVE TO THE STUB STACK IN BATHROOM TO LOFT IN ORDER TO PROVIDE FOR A VENTED SYSTEM. CONNECT TO EXISTING SOIL AND VENT PIPE. SOIL PIPE TO BE EXTENDED UP TO 900MM ABOVE WINDOW OPENING WHERE FOUND TO BE WITHIN 3M OF THE WINDOW.												
5. DORMER CONSTRUCTION												
WHERE DORMER IS CONSTRUCTED THEN THIS IS FORMED OF 125MM X 50MM STUDWORK AT 400MM C/C ON A 125MM X 50MM BASE PLATE. THE EXTERIOR OF THE FRAME TO HAVE 12.5MM THICK EXTERIOR GRADE PLY WITH ADDITIONAL 6MM SUPALUX OR FIRELINE BOARD TO THE DORMER CHEEKS WITHIN 1M OF ADJOINING PROPERTY. FIX REDLAND PLAIN VERTICAL HANGING TILES ON FELT AND BATTENS TO THE EXTERIOR OF THE DORMER FRAME (OR OTHER APPROVED LEAD SHEET OR CLADDING/SHIPLAP PVC. INFILL THE DORMER STUD FRAME WITH 112MM CELOTEX . INNER FACE OF DORMER AND RAFTER SLOPES AND PARTITION FORMING ROOM TO HAVE 12.5MM FOIL BACKED PLASTERBOARD AND SKIM COAT. DORMER TO HAVE CODE 4 LEAD FLASHING AT DORMER AND ROOF ABUTMENT.												
6.DORMER ROOF (OPTIONAL)												
WARM DECK ROOF TO DORMER TO HAVE 13MM HOT BITUMEN-BONDED SOLAR REFLECTIVE CHIPPINGS ON 3 LAYERS OF HIGH PERFORMANCE BUILT UP ROOFING FELT TO BS747 CLASS 2 OR 3 HOT LAID BY SPECIALIST. FELT LAID ON PERFORATED UNDERLAY OF SINGLE PLY FELT TYPE 3G HAVING 25MM HOLES AND PARTIALLY BONDED TO 115MM CELOTEX TD 3115 INSULATION BOARD LAID TO MANUFACTURERS REQUIREMENTS ON FIRRING PIECES(1:60 FALL) ON MINIMUM 150MM X 50MM GRADE SC3 SOFTWOOD TREATED JOISTS AT 400MM C/C.												
COLD FLAT DORMER ROOF												
(IMPOSED LOAD MAX 1.0 KN/M² - DEAD LOAD MAX 0.75 KN/M²) TO ACHIEVE U VALUE OF 0.18 W/M²K VENTILATED FLAT ROOF TO STRUCTURAL ENGINEER'S DETAILS, CONSTRUCTION COMPRISING OF 12.5MM SPA SOLAR REFLECTIVE CHIPPINGS TO ACHIEVE AA DESIGNATED FIRE RATING FOR SURFACE SPREAD OF FLAME BEDDED IN BITUMEN ON THREE LAYER FELT TO BS 6229:2003 LAID ON 22MM EXTERIOR GRADE PLYWOOD ON FIRRINGS TO GIVE A 1:40 FALL, FIXED TO 47 X 145MM GRADE C24 TIMBER JOISTS AT 400 CENTRES MAX SPAN 3.22M. CROSS VENTILATION TO BE PROVIDED ON OPPOSING SIDES BY A PROPRIETARY EAVES VENTILATION STRIP EQUIVALENT TO 25MM CONTINUOUS WITH FLY PROOF SCREEN. FLAT ROOF INSULATION IS TO BE CONTINUOUS WITH THE WALL INSULATION BUT STOPPED BACK TO ALLOW A 50MM AIR GAP ABOVE THE INSULATION FOR VENTILATION. INSULATION TO BE 90MM CELOTEX GA4000 BETWEEN JOISTS AND 62.5MM CELOTEX PL4000 INSULATED PLASTERBOARD WITH A VAPOUR BARRIER UNDER JOISTS. FINISH WITH A 3MM PLASTER SKIM. PROVIDE RESTRAINT TO FLAT ROOF BY FIXING USING OF 30 X 5 X 1000MM MS GALVANISED LATERAL RESTRAINT STRAPS AT MAXIMUM 2000MM CENTRES FIXED TO 100 X 50MM WALL PLATES AND ANCHORED TO WALL. WORKMANSHIP TO COMPLY TO BS 8000:4..												
7.MEANS OF ESCAPE AND FIRE RESISTANCE												
THE HABITABLE LOFT ROOMS ARE TO HAVE ½ HOUR FIRE RESISTING DOORS ALONG WITH SELF CLOSING DEVICES AND 25MM DOOR STOPPERS. EXISTING DOORS OFF THE HALLWAY STAIRWELL TO ALL HABITABLE ROOMS INCLUDING KITCHEN TO HAVE DOORS FITTED WITH SELF CLOSING DEVICES AND 25MM DOOR STOPPERS. NO GLAZING IN THE STAIRWELL, BUT WHERE FITTED THEN SHOULD BE GEORGIAN WIRED GLASS. THE LOFT LOBBY, FIRST FLOOR AND GROUND FLOOR (PLUS BASEMENT, WHERE FOUND) ARE TO HAVE A SMOKE DETECTOR AT EACH OF THE LEVELS. THEY SHOULD BE MAINS OPERATED WITH BATTERY BACK UP AND BE INTER CONNECTED. THE NEW JOISTS IN THE LOFT FLOOR ARE TO HAVE 100MM ROCKWOOL INSULATION LAID ON WIRE NETTING TACKED TO THE SIDES OF THE JOISTS.												
FLOORING BOARDS ARE TO BE 18MM TONGUED AND GROOVED OR HAVE 3MM THICK HARDBOARD OVER STRAIGHT EDGED BOARDS.												
FIRE RESISTANCE TO STEEL BEAMS TO BE 1 HOUR MINIMUM AND BE ACHIEVED BY INTUMESCENT PAINT OR 2 LAYERS OF 12.5MM PLASTERBOARD WIRE BOUND AT 100MM CENTRES AND THEN 10MM THICK GYPSUM PLASTER FINISH.												
8.HEATING/HOT WATER												
HEATING/HOT WATER TO BE PROVIDED BY WALL HUNG BOILER, WHERE RENEWED, AND HAVING FAN ASSISTANCE WITH SEDBUC RATING OF NOT MORE THAN 78. THERE SHOULD BE A PROGRAMMER AND ROOM STAT ALONG WITH THERMOSTATIC RADIATOR VALVES. HEATING TO BE FITTED BY A CORGI REGISTERED CONTRACTOR.												
9.PARTITIONS												
PARTITIONS TO LOFT AND AROUND STAIRWELL ARE TO BE CONSTRUCTED WITH 100MM X 50MM STUD WORK AT 400MM C/C AND HAVING 12.5MM THICK PLASTERBOARD/SKIM EITHER SIDE. INFILL WITH 100MM ROCKWOOL INSULATION.												
DOUBLE UP FLOOR JOISTS UNDER PARITIONS.												
FRONT DWARF PARTITION BELOW ORIGINAL PURLIN TO BE FORMED WITH 125MM X 50MM AT 400MM C/C STUDWORK WITH 112MM CELOTEX INFILL AND 12.5MM FOIL BACKED PLASTERBOARD WHICH IS ALSO FIXED TO THE FRONT SLOPES.												
10.ELECTRICAL												
PRIOR TO COMPLETION THE LOCAL AUTHORITY SHOULD BE SATISFIED THAT ANY SUCH WORK (OTHER THAN THAT DEFINED AS MINOR WORK) COMPLIES WITH PART P.												
THIS WITH REQUIRE AN APPROPRIATE BS 7671 ELECTRICAL INSTALLATION CERTIFICATE TO BE ISSUED BY A PERSON AUTHORISED TO DO SO (I.E. A PERSON WHO IS REGISTERED UNDER A RECOGNISED COMPETENT PERSONS SCHEME FOR SELF-CERTIFICATION.)												
11.THERMAL INSULATION TO FRONT ROOF SLOPE												
THE FRONT RAFTERS SHOULB BE INCREASED IN DEPTH TO 150MM BY THE INTRODUCTION OF 150MM X 50MM RAFTERS BETWEEN THE RIDGE AND FRONT DWARF PARTITION.												
FIX 50MM CELOTEX BETWEEN RAFTERS TO FRONT ROOM AND A FURTHER 75MM CELOTEX ACROSS THE INNER FACE OF THE RAFTERS IN ORDER THAT A TOTAL OF 125MM THICK CELOTEX INSULATION BOARD IS ACHIEVED.												
JUNCTION OF THE COLD ROOF TO THE FRONT SLOPES AND THE REAR DORMER WARM DECK FLAT ROOF TO BE SEALED AT RIDGE LEVEL WITH ROCKWOOL.												
A 50MM AIR GAP IS TO BE MAINTAINED TO THE FRONT ROOF SLOPE BETWEEN THE INSULATION AND TILES TO ALLOW AIR FLOW UNLESS YOU HAVE BREATHABLE FELI.												
THE FRONT ROOF SLOPE IS TO HAVE LOW LEVEL ROOF TILE VENTS AT 1.5M C/C WHERE THERE IS NO EAVES VENTILATION. AND HIGH LEVEL VENTS AT 1.5M C/C ARE TO BE PROVIDED NEAR RIDGE OR VENTILATED RIDGE TILES.												
A TOTAL OF 270MM THICK ROCKWOOL IS REQUIRED TO FRONT (AND/OR REAR) ROOF VOID LAID IN TWO LAYERS.												
12.GENERAL												
CHIMNEY STACKS TO ROOF ARE TO BE CONFIRMED WHETHER IN USE. THE CHIMNEY STACK, IF IN USE SHOULD BE RAISED ABOVE THE ROOF OF THE DORMER. OTHERWISE SEAL OFF THE STACK BY REMOVING POTS AND BEDDING SLATE/TILES IN MORTAR. MAKE SURE THAT YOU HAVE THE NEIGHBOUR'S PERMISSION FOR SHARED STACKS BEFORE WORK COMMENCES.												
THE CHIMNEY FLUES INTERNALLY MUST BE MADE UNUSABLE BY REMOVING OR SEALING OFF IN BRICKWORK.												
NO STEEL BEAM OR SPREADER PLATE IS TO BE IN CHIMNEY FLUE BRICKWORK.												
ANY RESIDUE OF CHIMNEY FLUE BRICKWORK IN THE LOFT AREA IS TO BE SUPPORTED UPON 3 NOS. 18 INCH GALLOWS BRACKETS WITH 75MM ANGLE IRON WELDED TO THE ENDS AND A 6MM METAL SHEET ACROSS THE FRAME CREATED.												
THE HEIGHT OF BRICKWORK BELOW THE RIDGE LEVEL SHOULD NOT BE LESS THAN THE HEIGHT OF THE STACK ABOVE THE ROOF RIDGE.												
DORMER CHEEKS TO BE BUILT UP OFF OF 3 NOS. 170MM X 50MM RAFTERS BOLTED TOGETHER.												
FLOORING JOISTS TO BE NOGGED AT 1.5M C/C.												
REFERENCE DRAWINGS		NOTES PLEASE NOTE THAT BEFORE BUILDING WORKS COMMENCES IT IS THE RESPONSIBILITY OF THE BUILDER OR OWNER TO SERVE PARTY WALL NOTICES TO ALL NEIGHBORS	No	DATE	REVISION	BY	CHK	CONSULTANT	DRAWN F.R	CLIENT/PROJECT		DRAWING No.
								CIVIL CONSULTING LTD. CIVIL ENGINEERS STRUCTURAL ENGINEERS ARCHITECTURAL DESIGNERS Contact: 07947249323	CHECKED A.R	THE FENS CRAYS HILL		D23
									PROJECT NO.	TITLE SPECIFICATIONS		SCALE: NTS @A3
												DATE: 04-11-2023